



INDICATIVE 3D FRONT OF HOUSE
SCALE

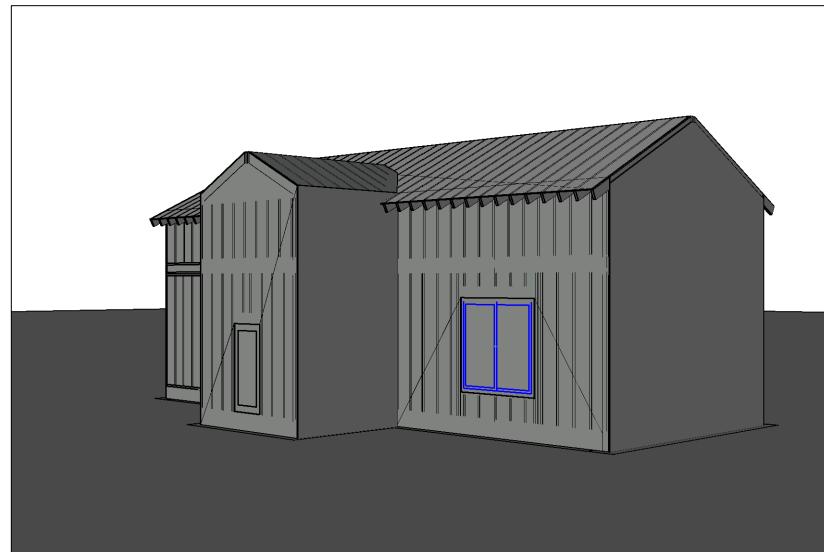

INDICATIVE 3D IMAGE 1
SCALE

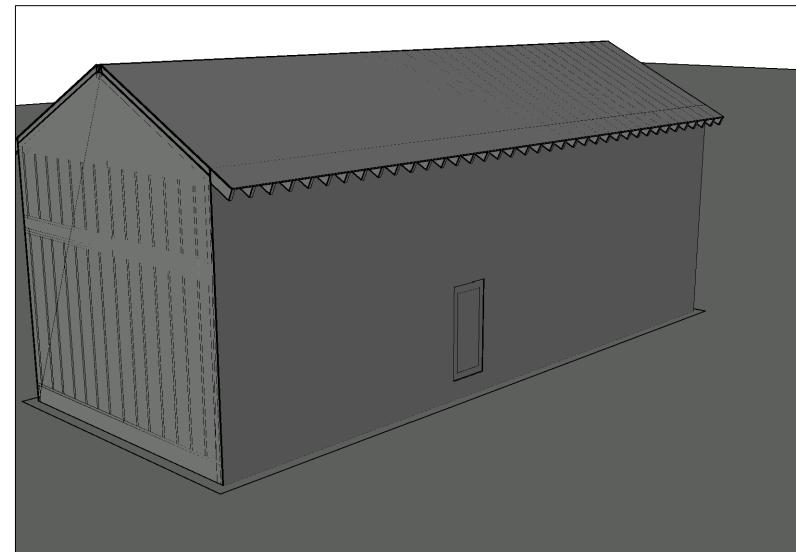


INDICATIVE 3D BACK OF HOUSE
SCALE

RESIDENTIAL PORTFOLIO BUILDING
CLIENT'S NAME: JOHN DOE
ADDRESS


No.	Revision/Issue	Date
NEW HOUSE		
ADDRESS LOCATION		
PROJECT # 00000001		
SHEET SIZE A1		
DATE 03/31/2025		
ISSUE BUILDING CONSENT		
DRAWING TITLE: ARCHITETURAL		
SHEET: DRAWING TITLE:		
A01		

RESIDENTIAL PORTFOLIO BUILDING

CLIENT'S NAME: JOHN DOE

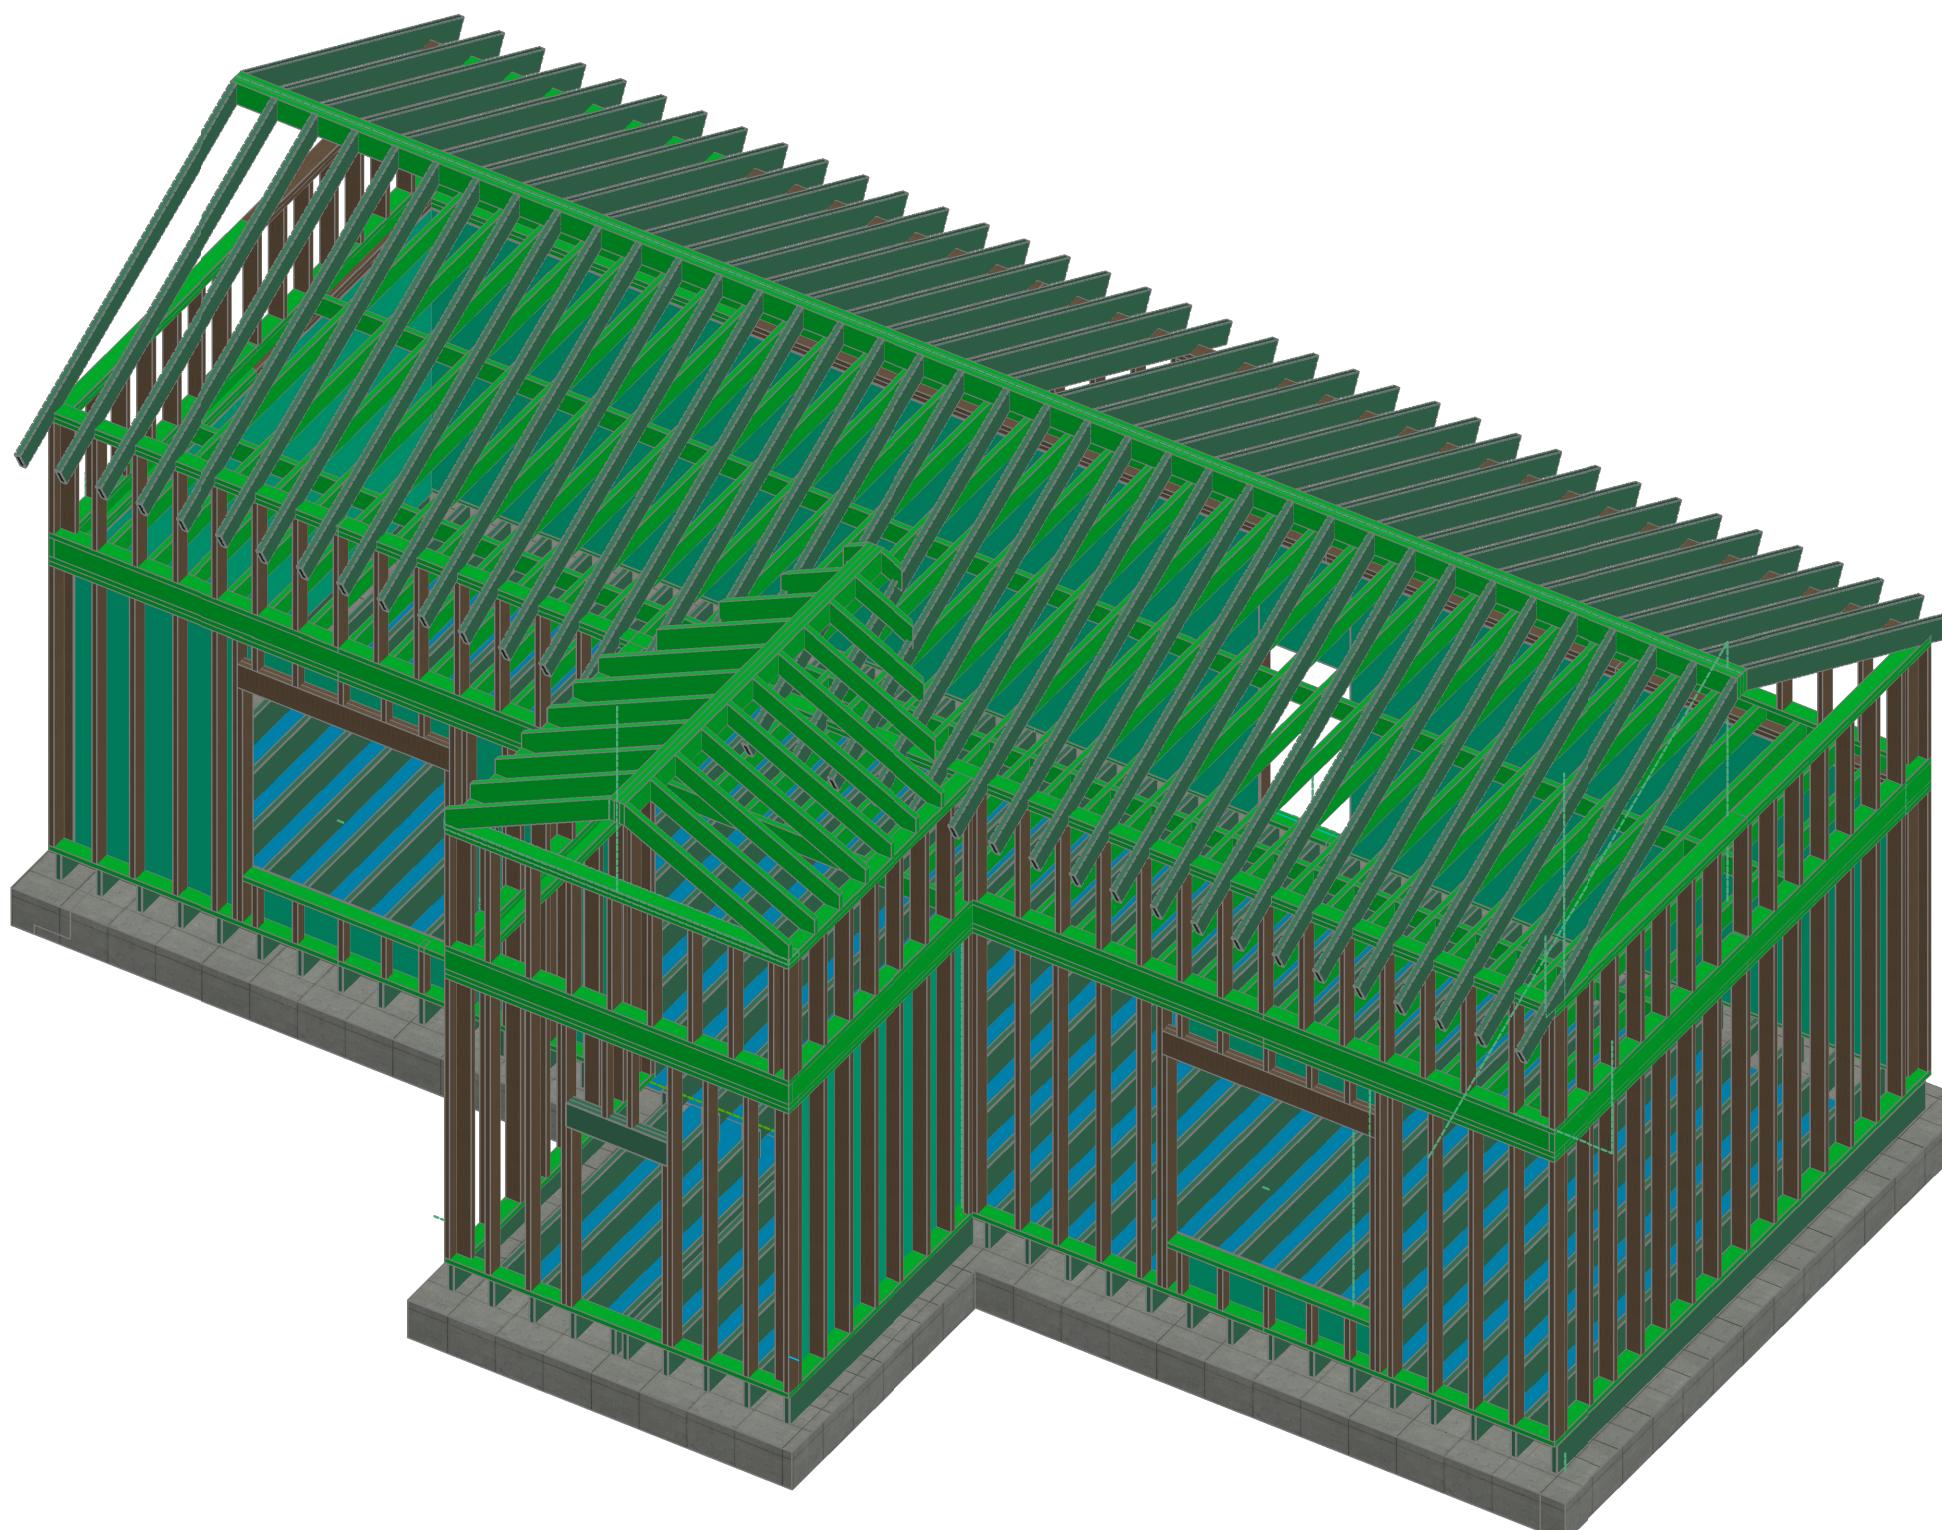

INDICATIVE 3D IMAGE 1

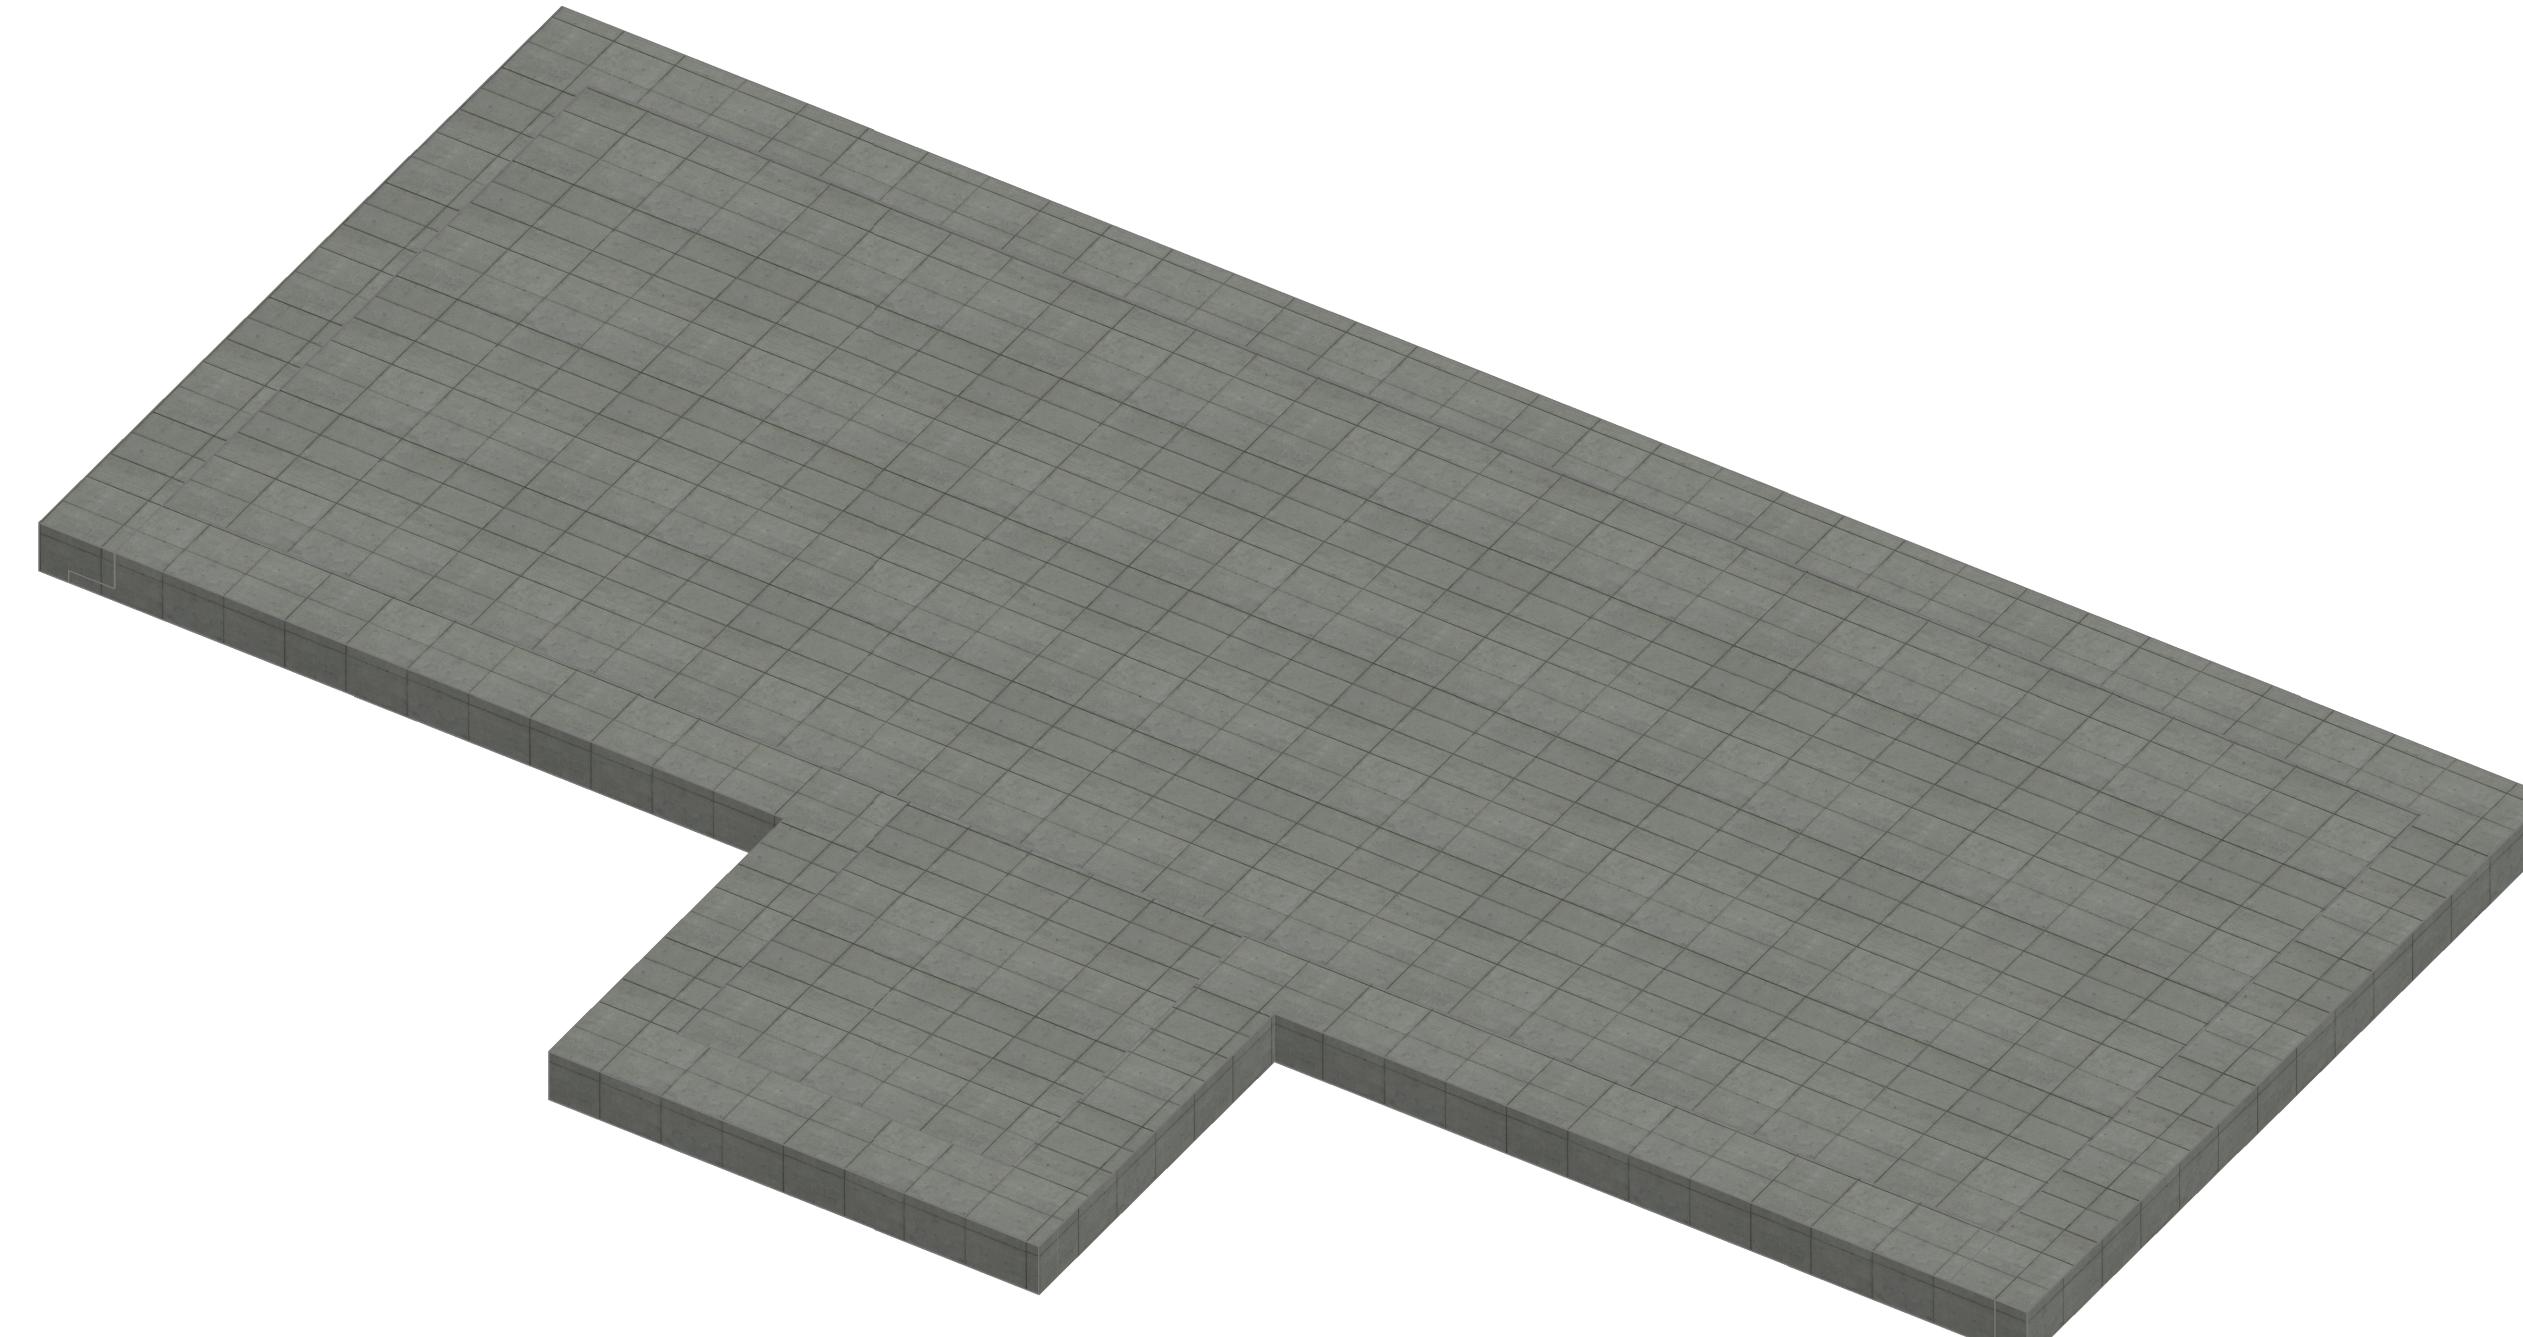

 INDICATIVE 3D IMAGE 2
SCALE



GENERAL NOTES:



UNLESS OTHERWISE INDICATED ALL DIMENSIONS ARE
GIVEN IN IMPERIAL- FEET & INCHES. DO NOT SCALE
OFF DRAWINGS.

The Design, information & technical detailing contained herein is copyright of structural engineer. any adaption, distribution, or any form of reproduction of these works, in any part or in their entirety is prohibited.


PROJECT INFORMATION

Territorial Authority: LOS ANGELES COUNTY

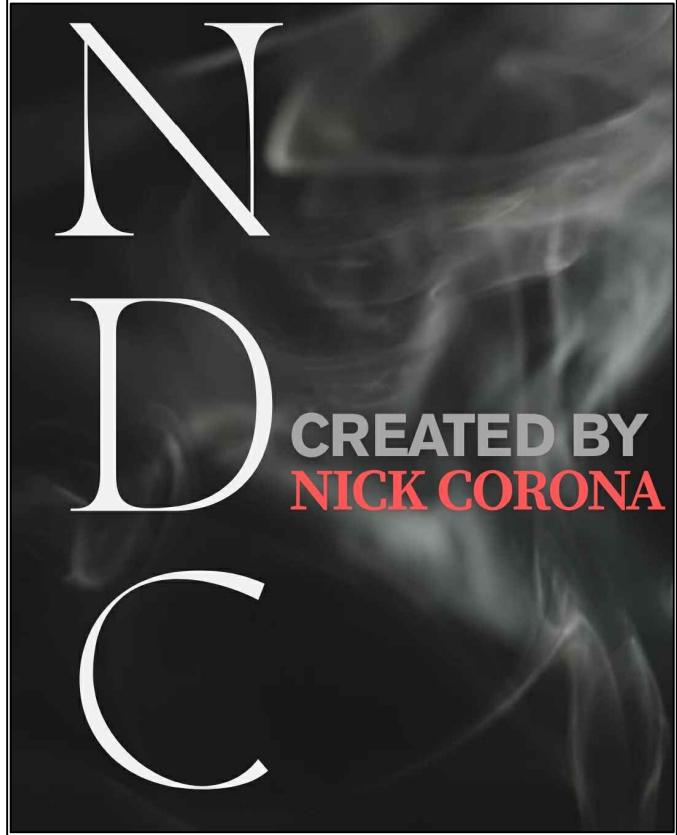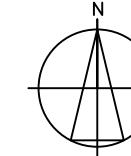No.	Revision/Issue	Date
 <p>CREATED BY NICK CORONA</p>		
<p>NEW HOUSE</p> <p>ADDRESS LOCATION</p>		
PROJECT #	00000001	
SHEET SIZE	A1	
DATE	03/31/2025	
ISSUE	BUILDING CONSENT	
		
DRAWING TITLE:		
STRUCTURAL		
SHEET:	DRAWING TITLE: S01	

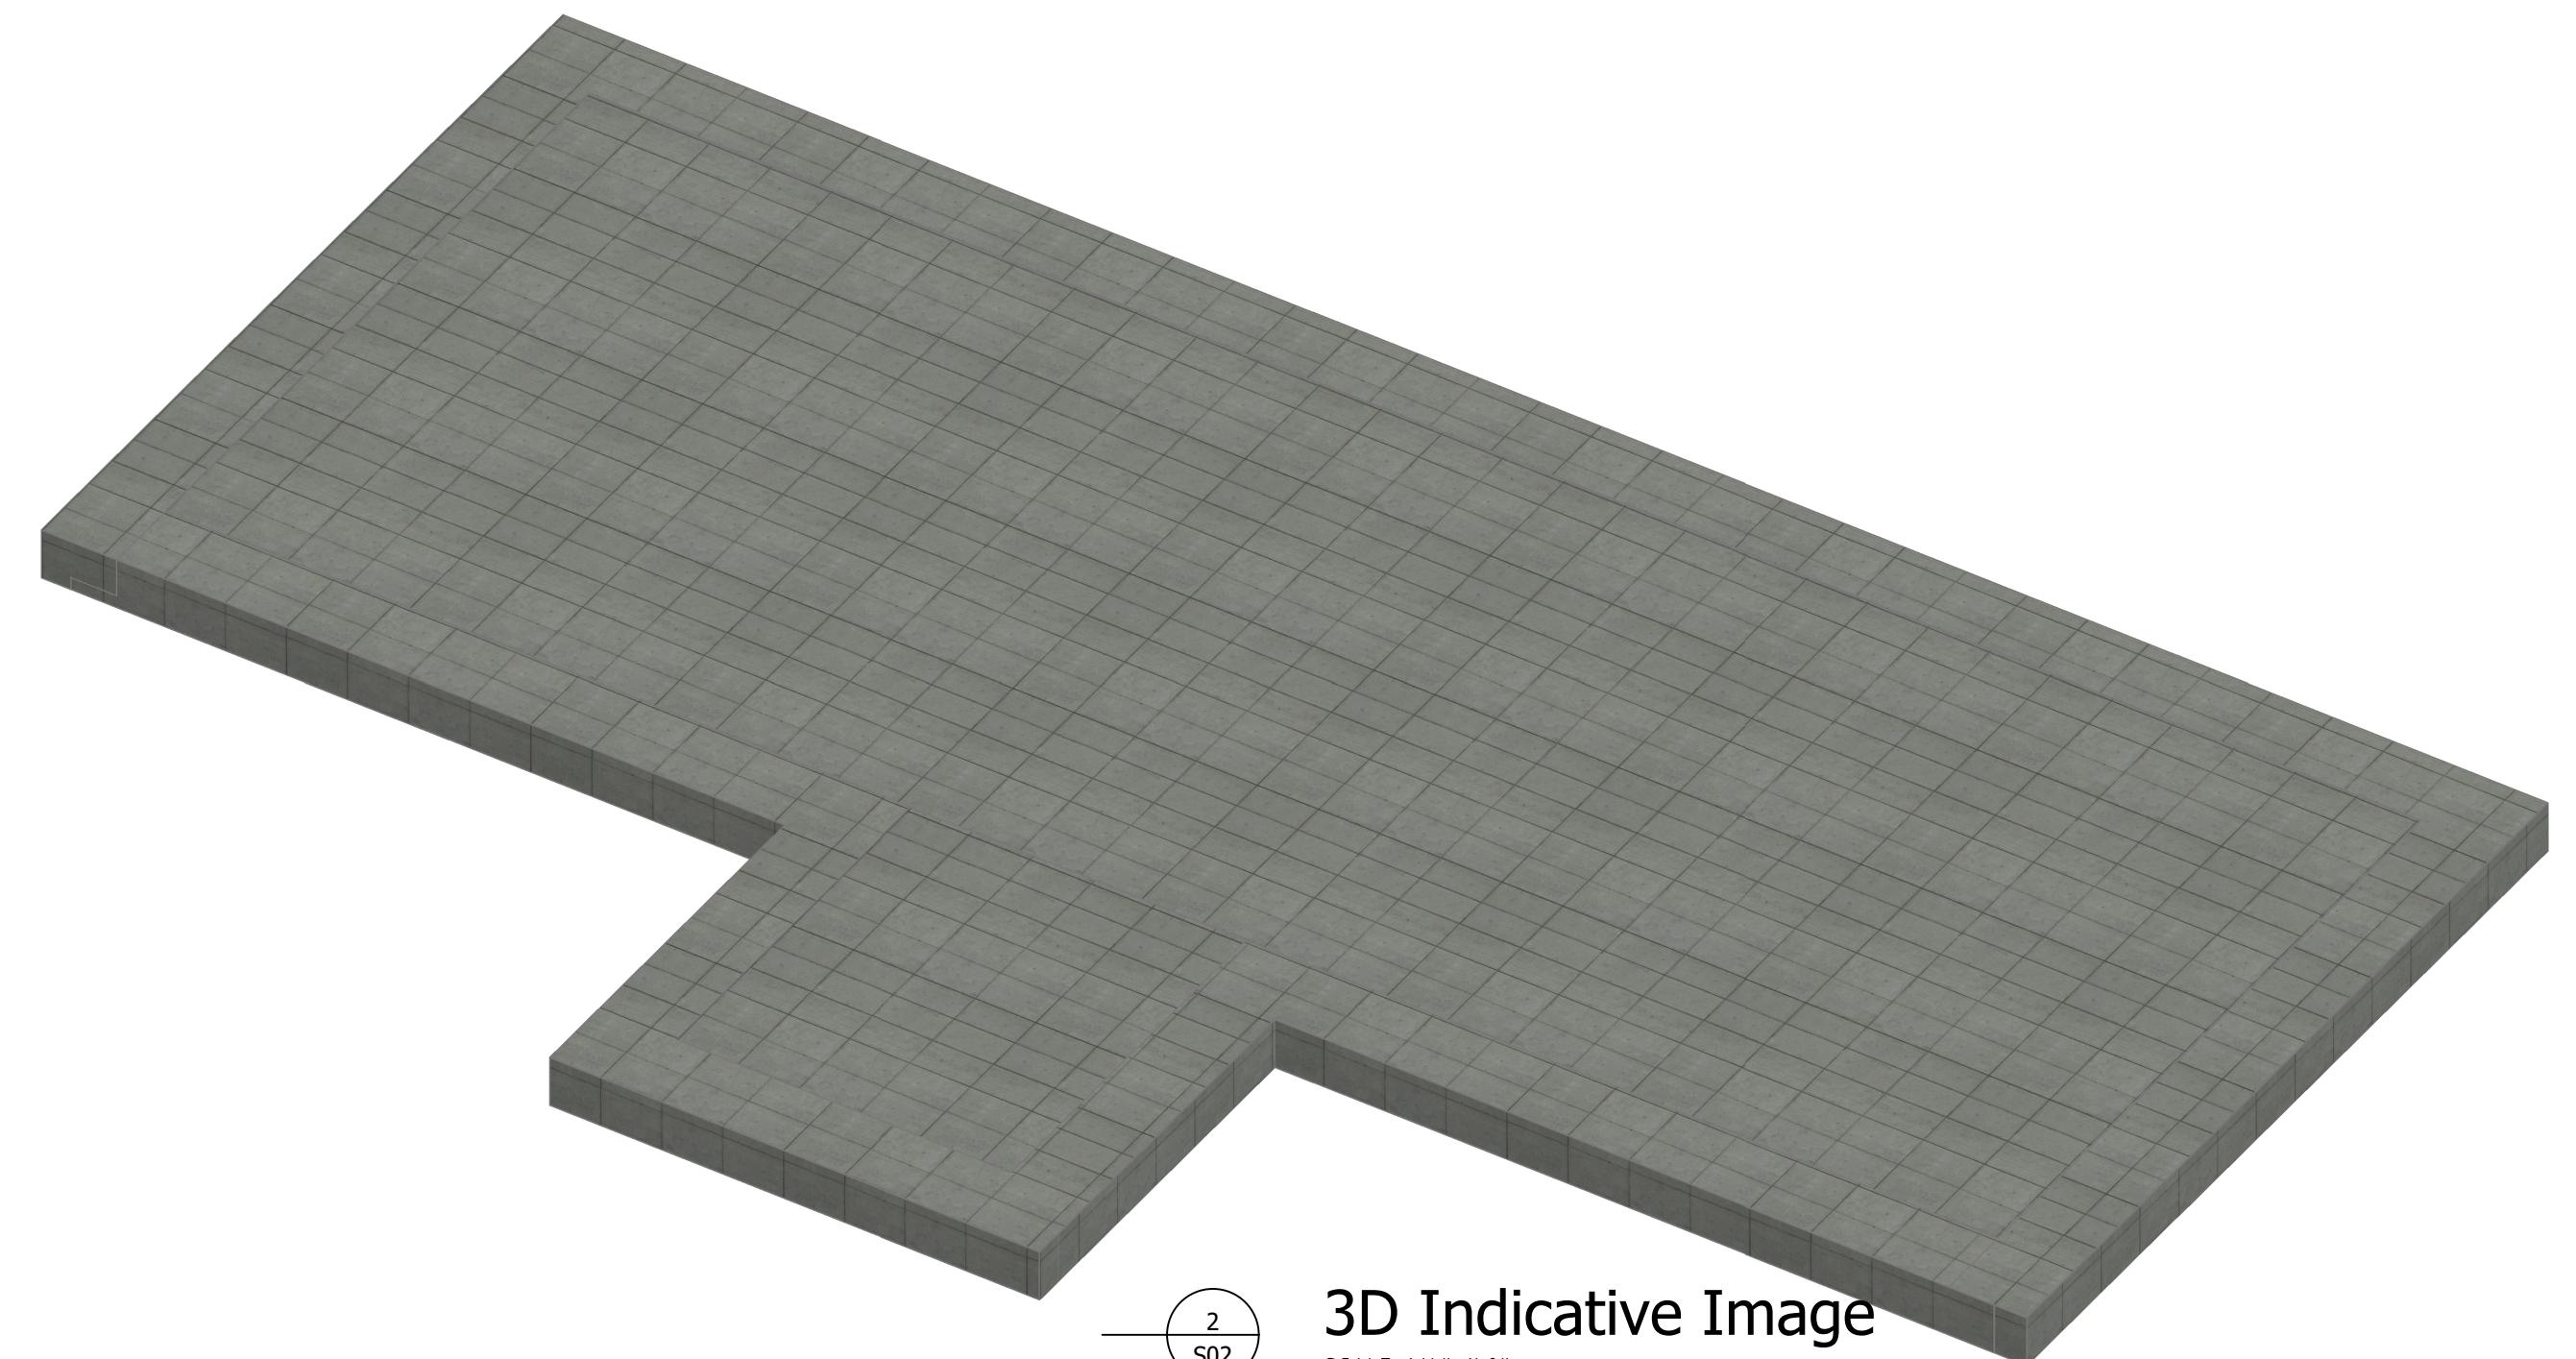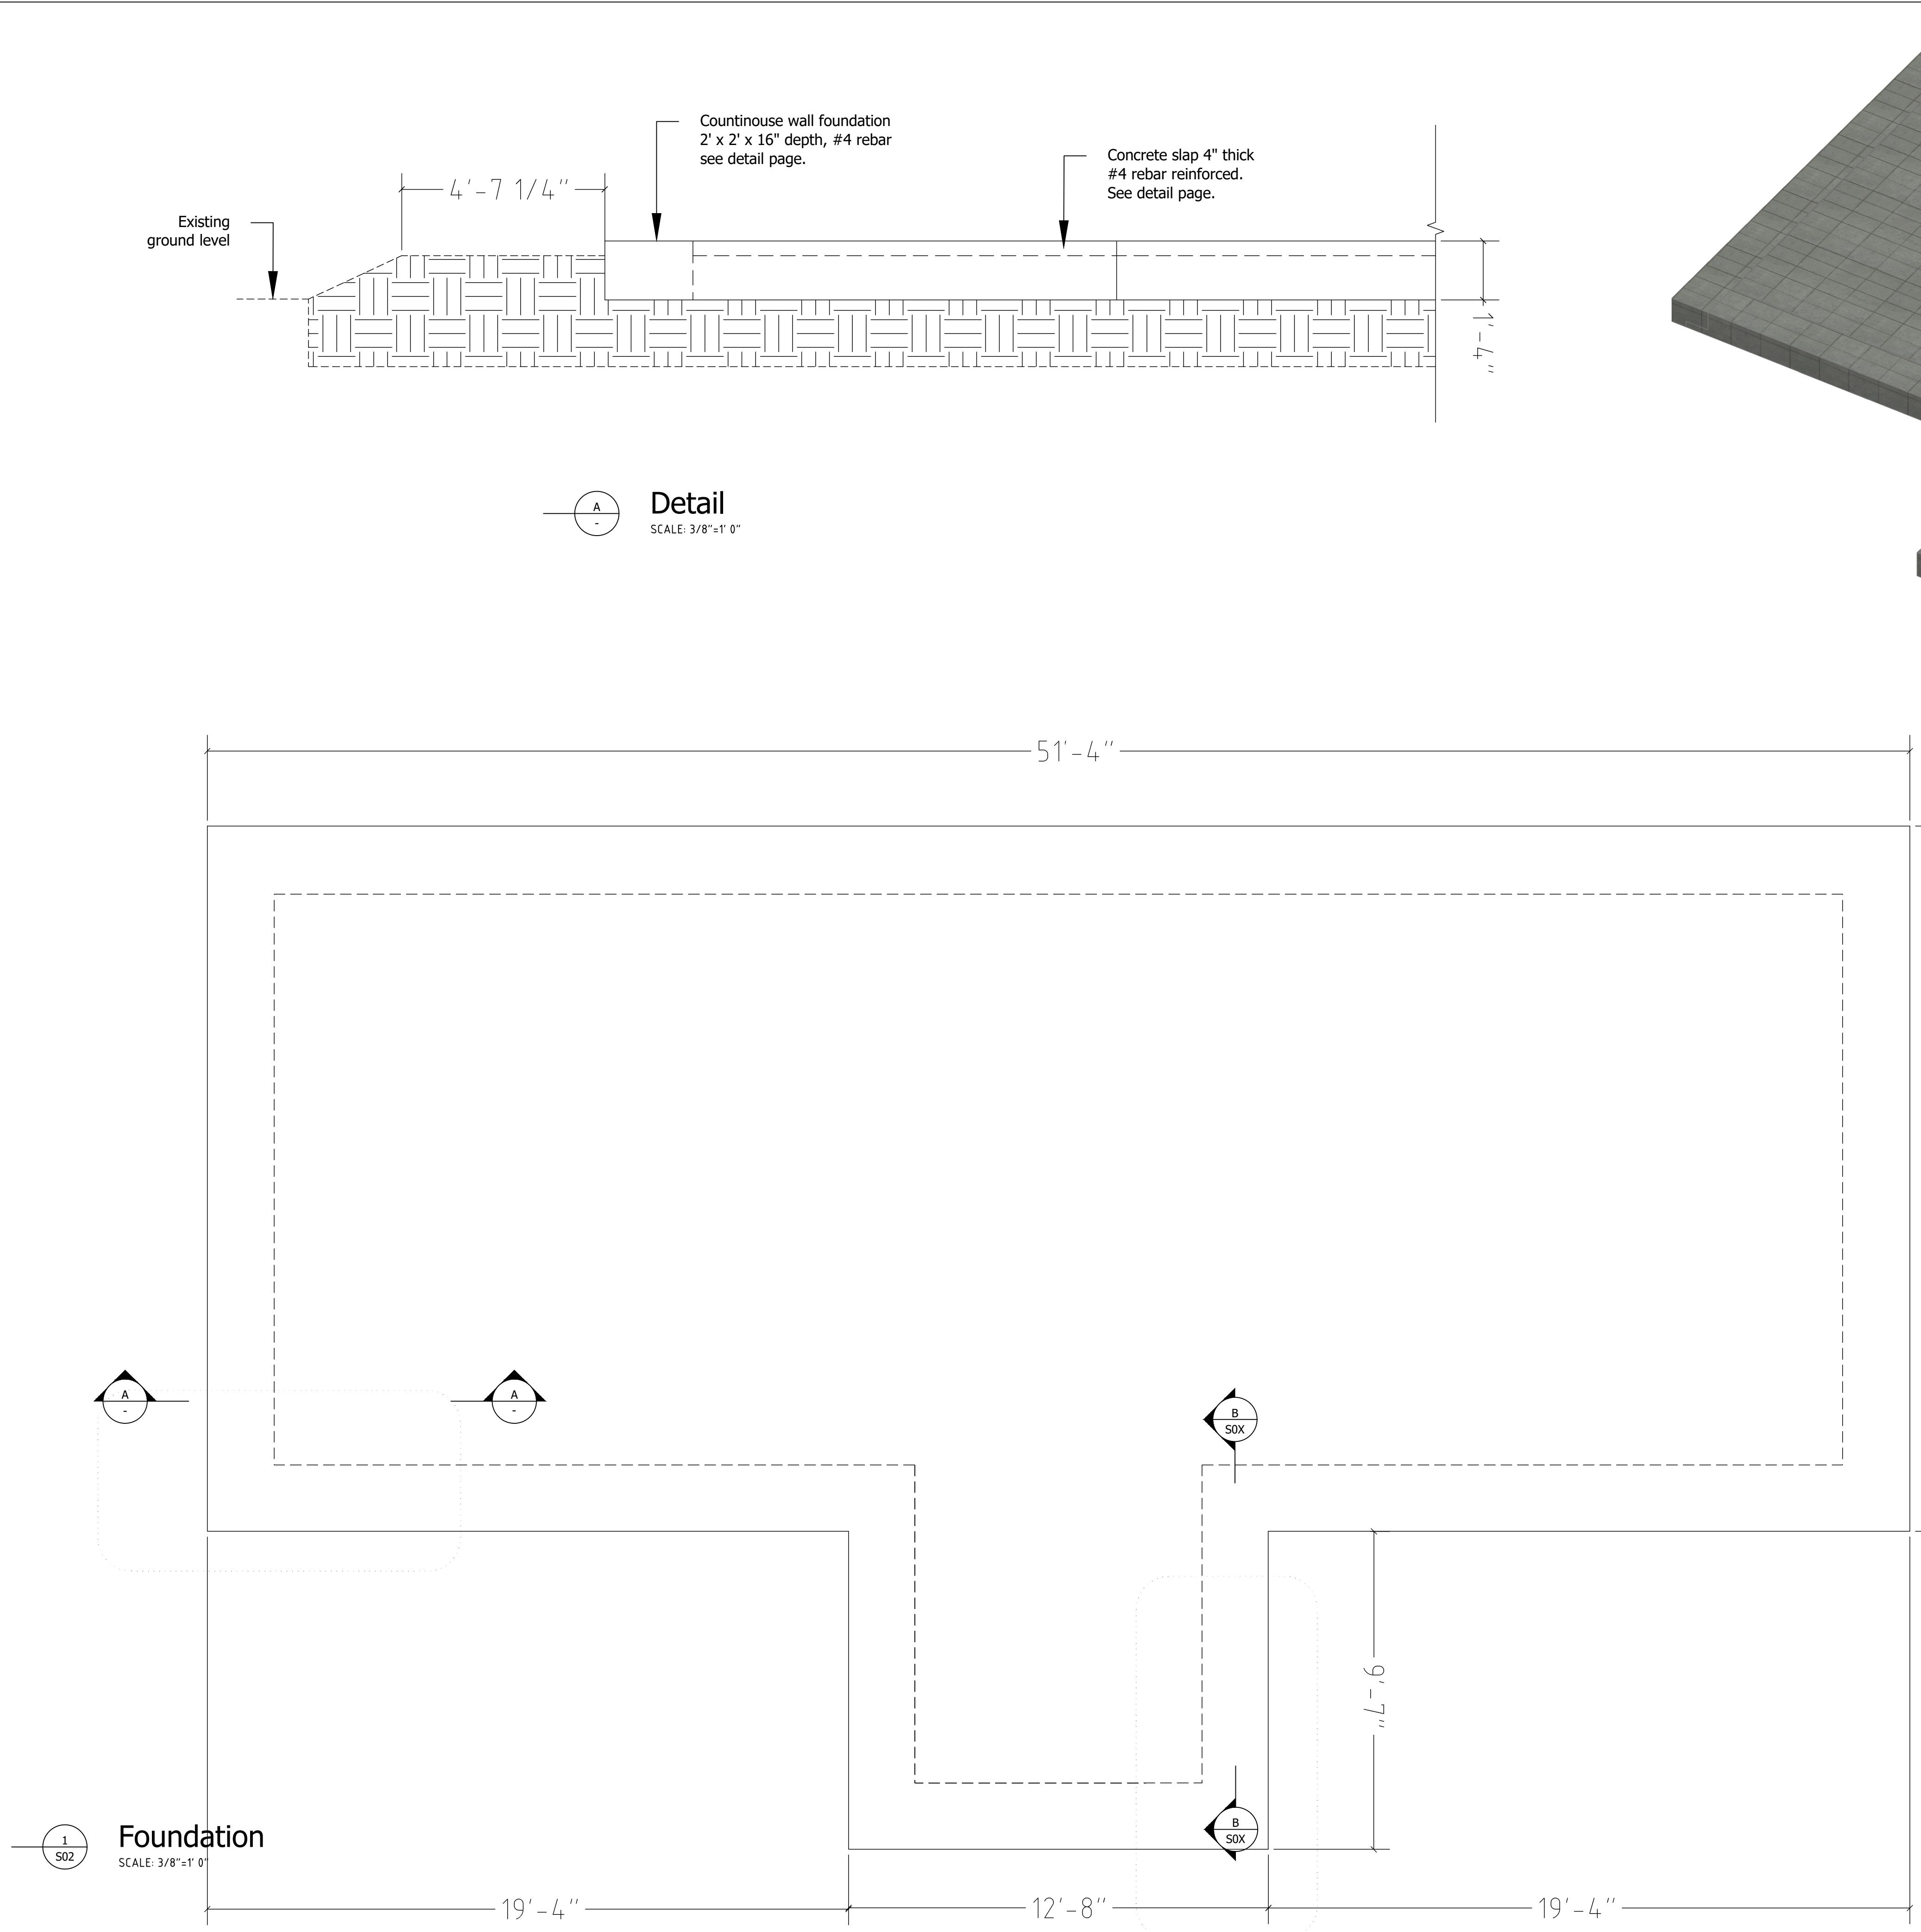


No.	Revision/Issue	Date
NDC CREATED BY NICK CORONA		
NEW HOUSE		
ADDRESS LOCATION		
PROJECT #	0000001	
SHEET SIZE	A1	
DATE	03/31/2025	
ISSUE	BUILDING CONSENT	
DRAWING TITLE:		
STRUCTURAL		
SHEET:	S02	
DRAWING TITLE:		

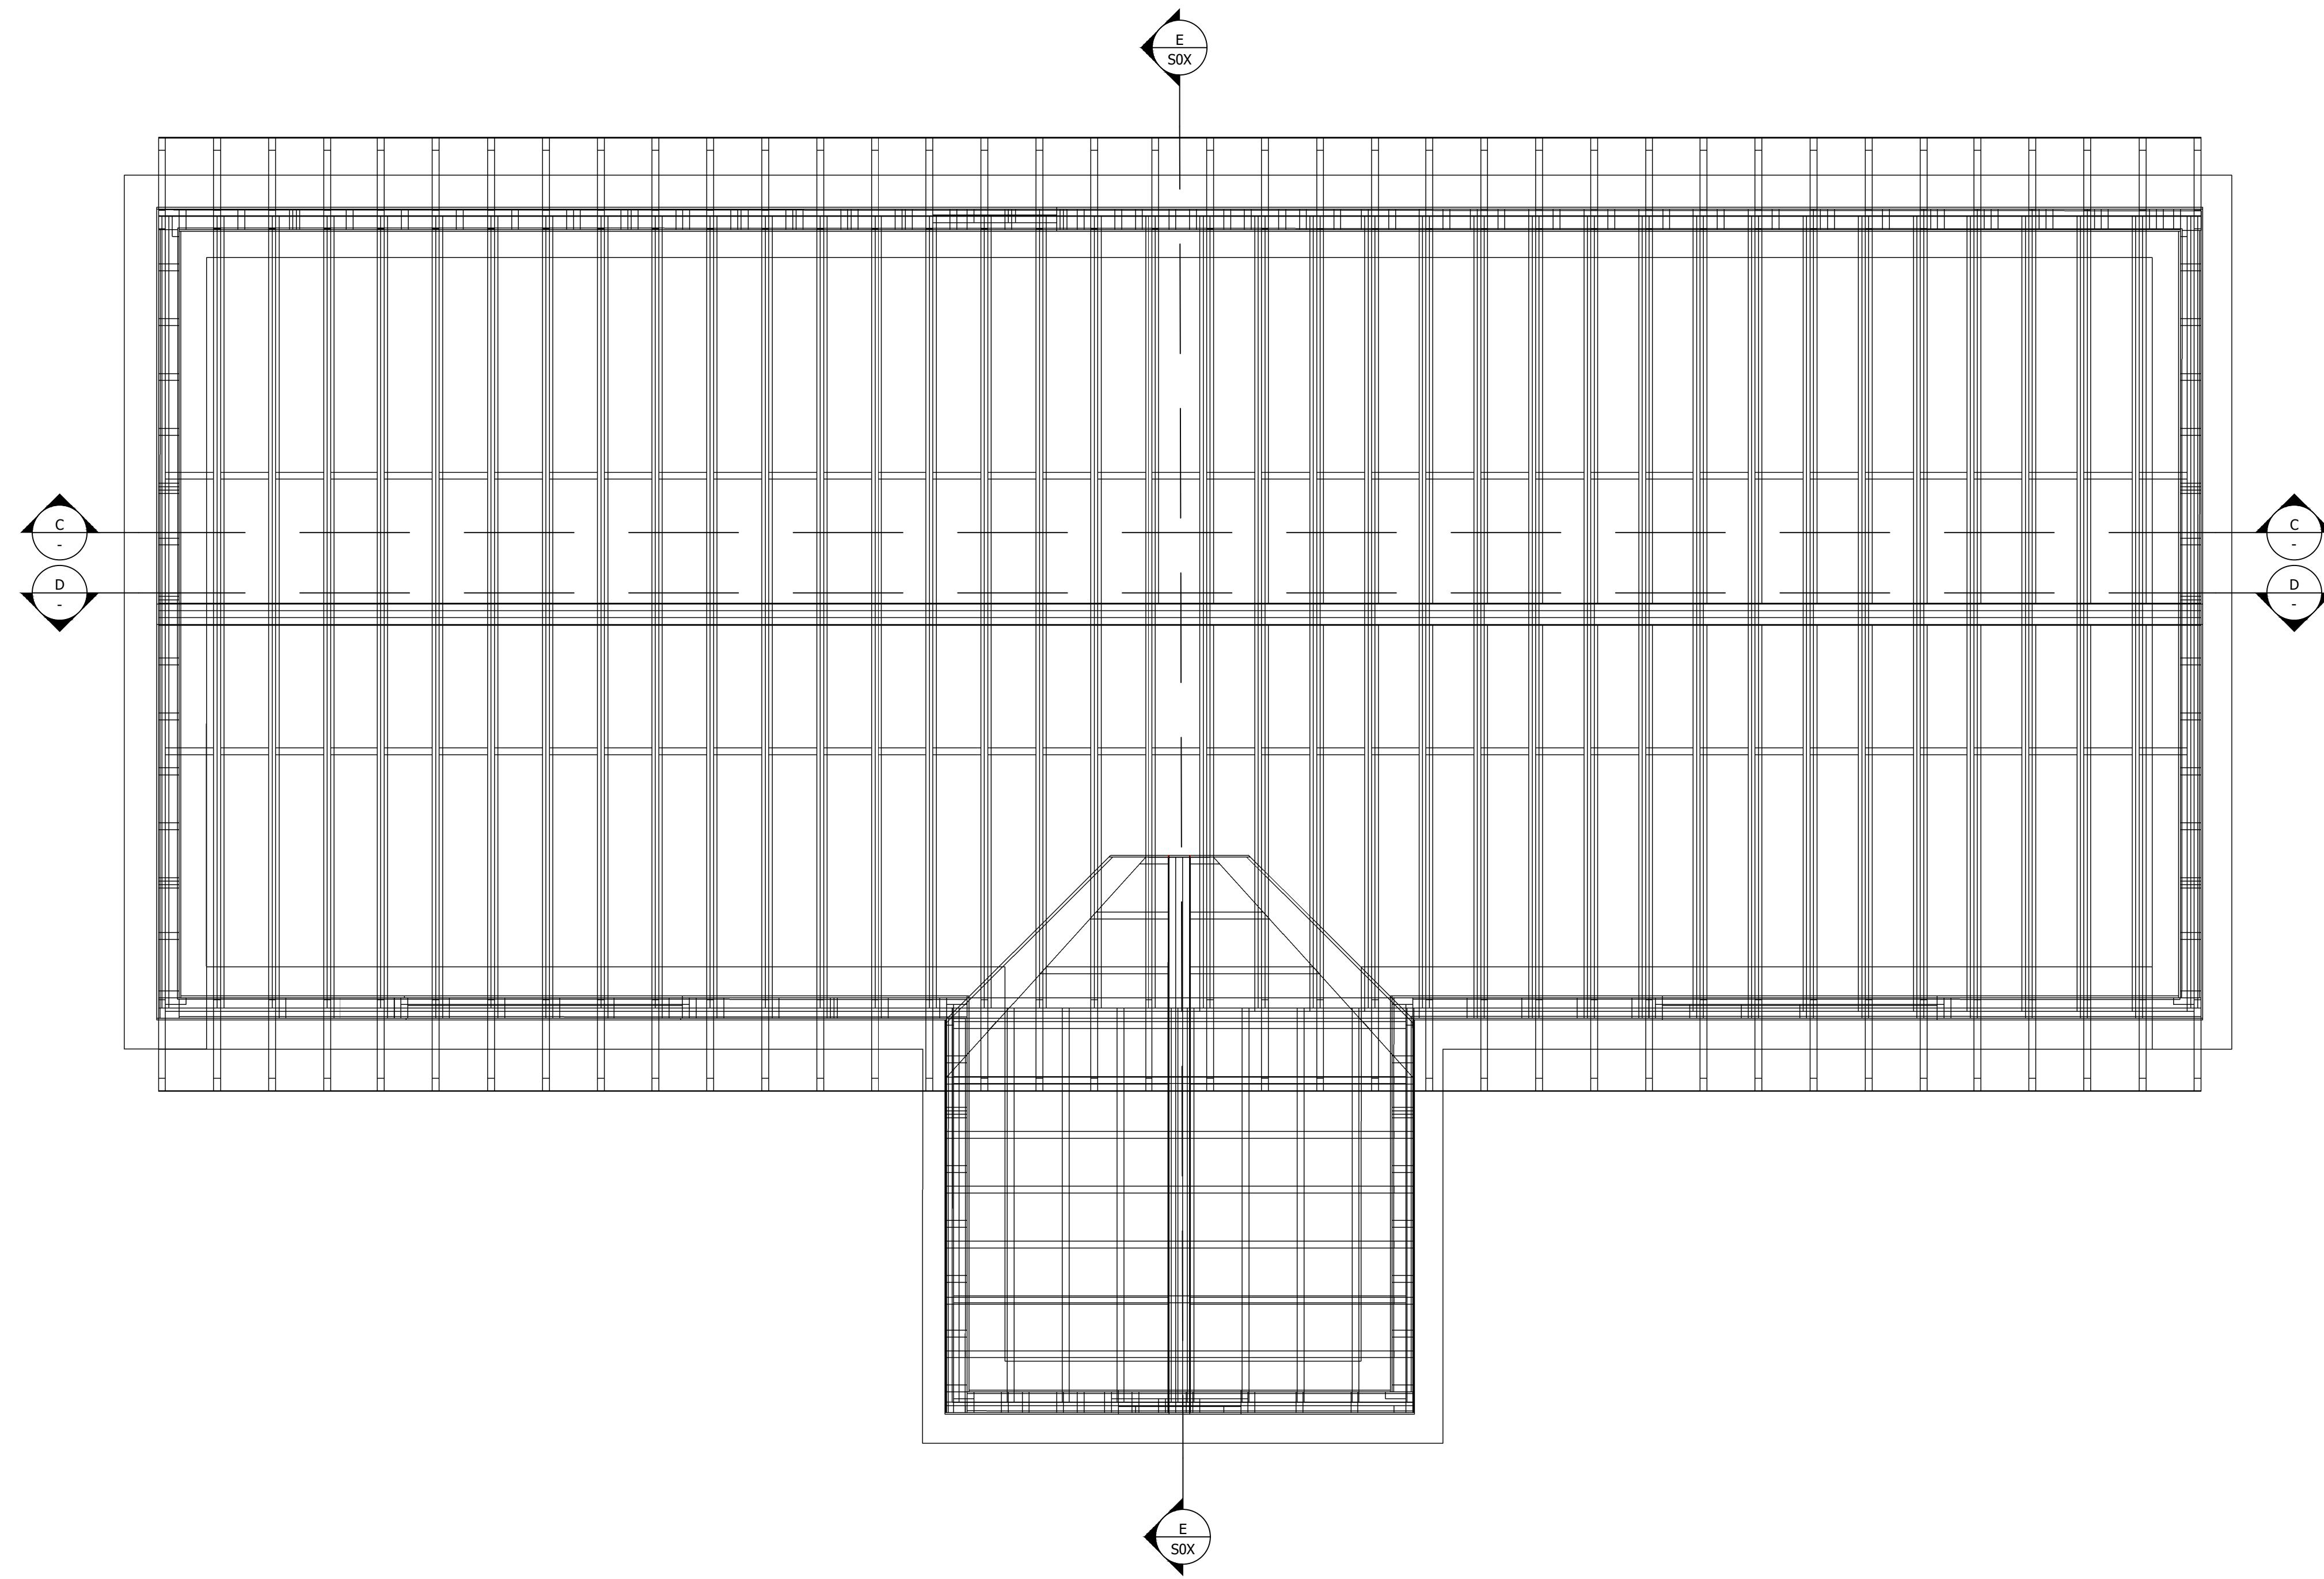

1
-


2D INDICATIVE TOP VIEW IMAGE
SCALE: 3/8"=1' 0"

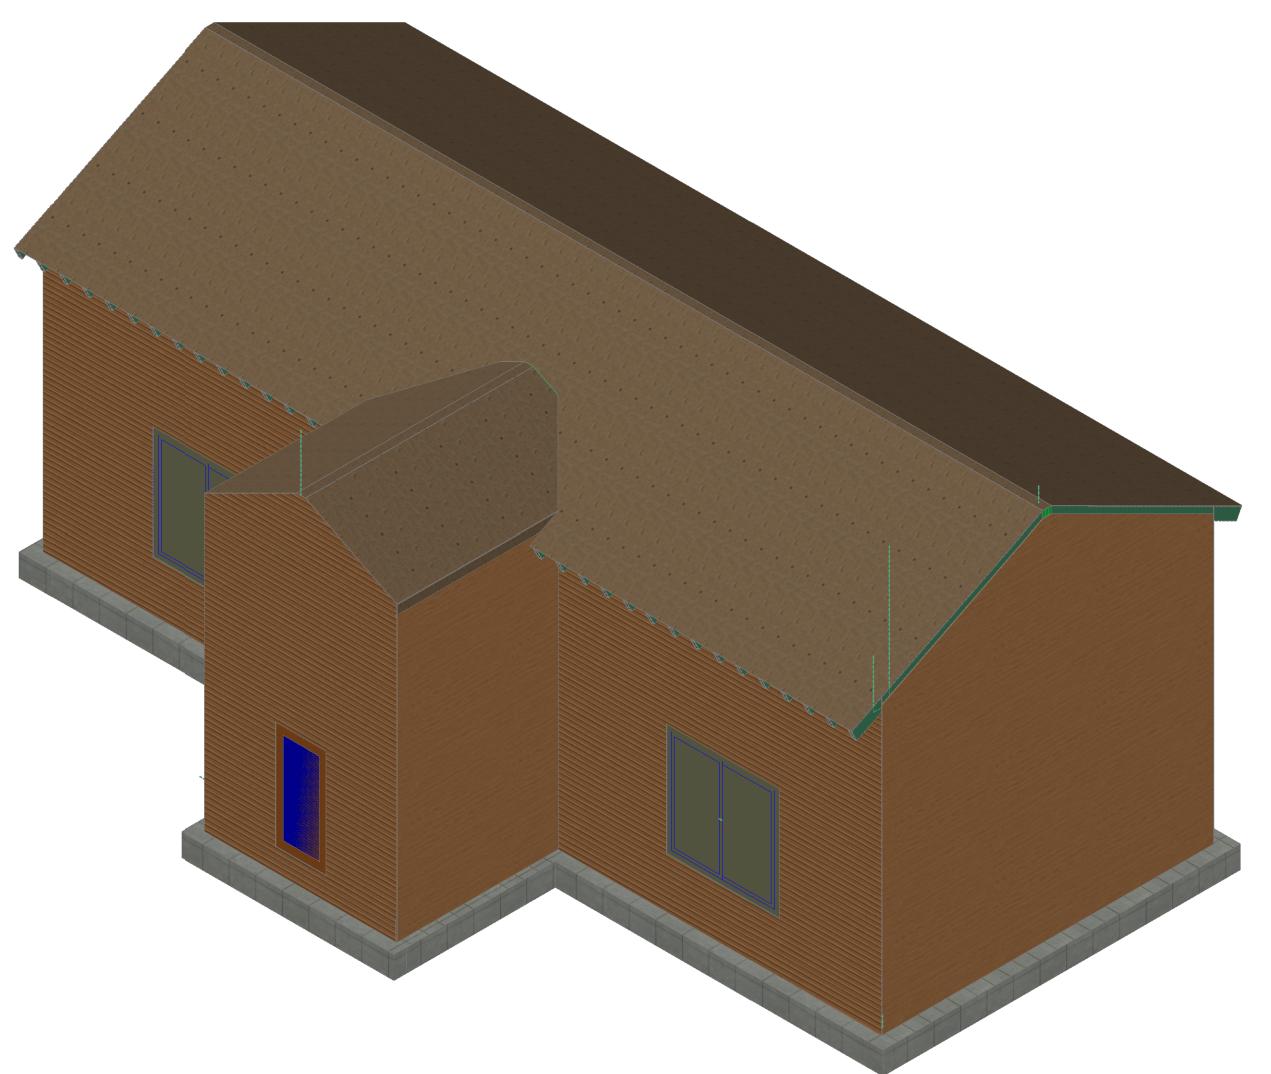


3D Indicative Image

SCALE: 1/4"=1' 0"

No.	Revision/Issue	Date
NEW HOUSE		
ADDRESS LOCATION		
PROJECT # 0000001 SHEET SIZE A1 DATE 03/31/2025 ISSUE BUILDING CONSENT		
DRAWING TITLE: STRUCTURAL SHEET: S03		
DRAWING TITLE:		

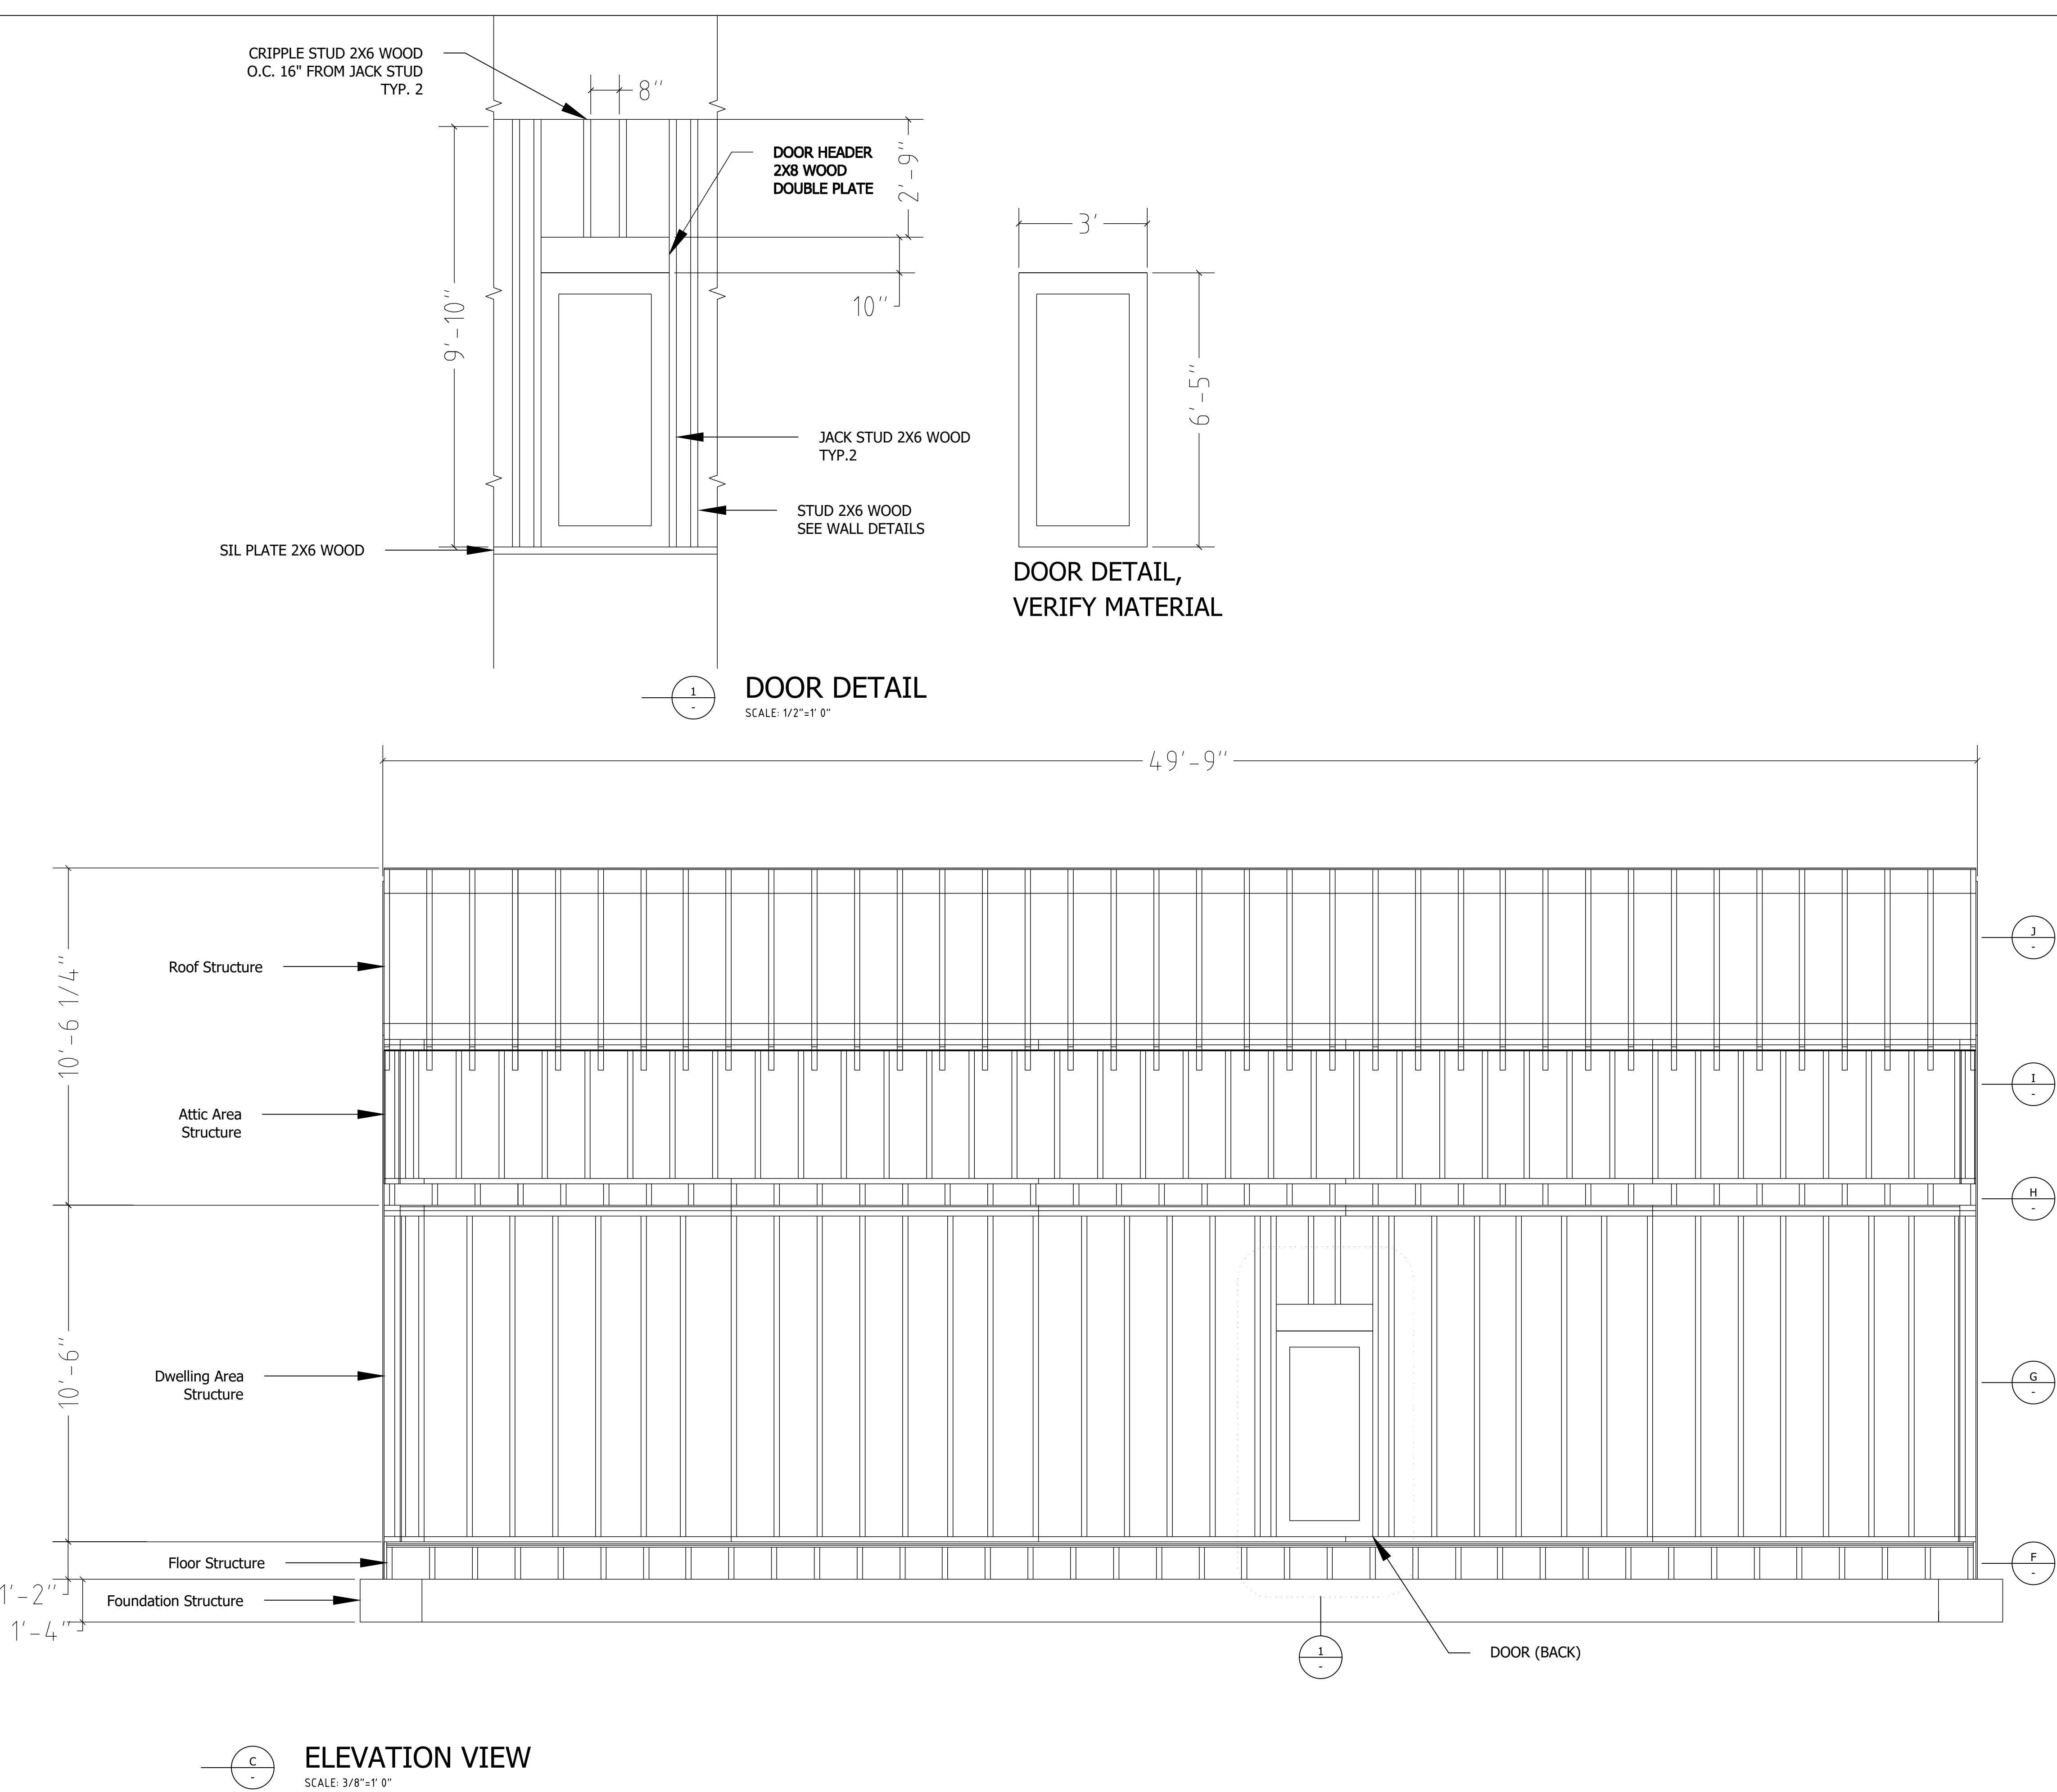


No.	Revision/Issue	Date
N C U N C		
CREATED BY NICK CORONA		
NEW HOUSE		
ADDRESS LOCATION		
PROJECT #	0000001	
SHEET SIZE	A1	
DATE	03/31/2025	
ISSUE	BUILDING CONSENT	
DRAWING TITLE:		
STRUCTURAL		
SHEET:	S04	
DRAWING TITLE:		

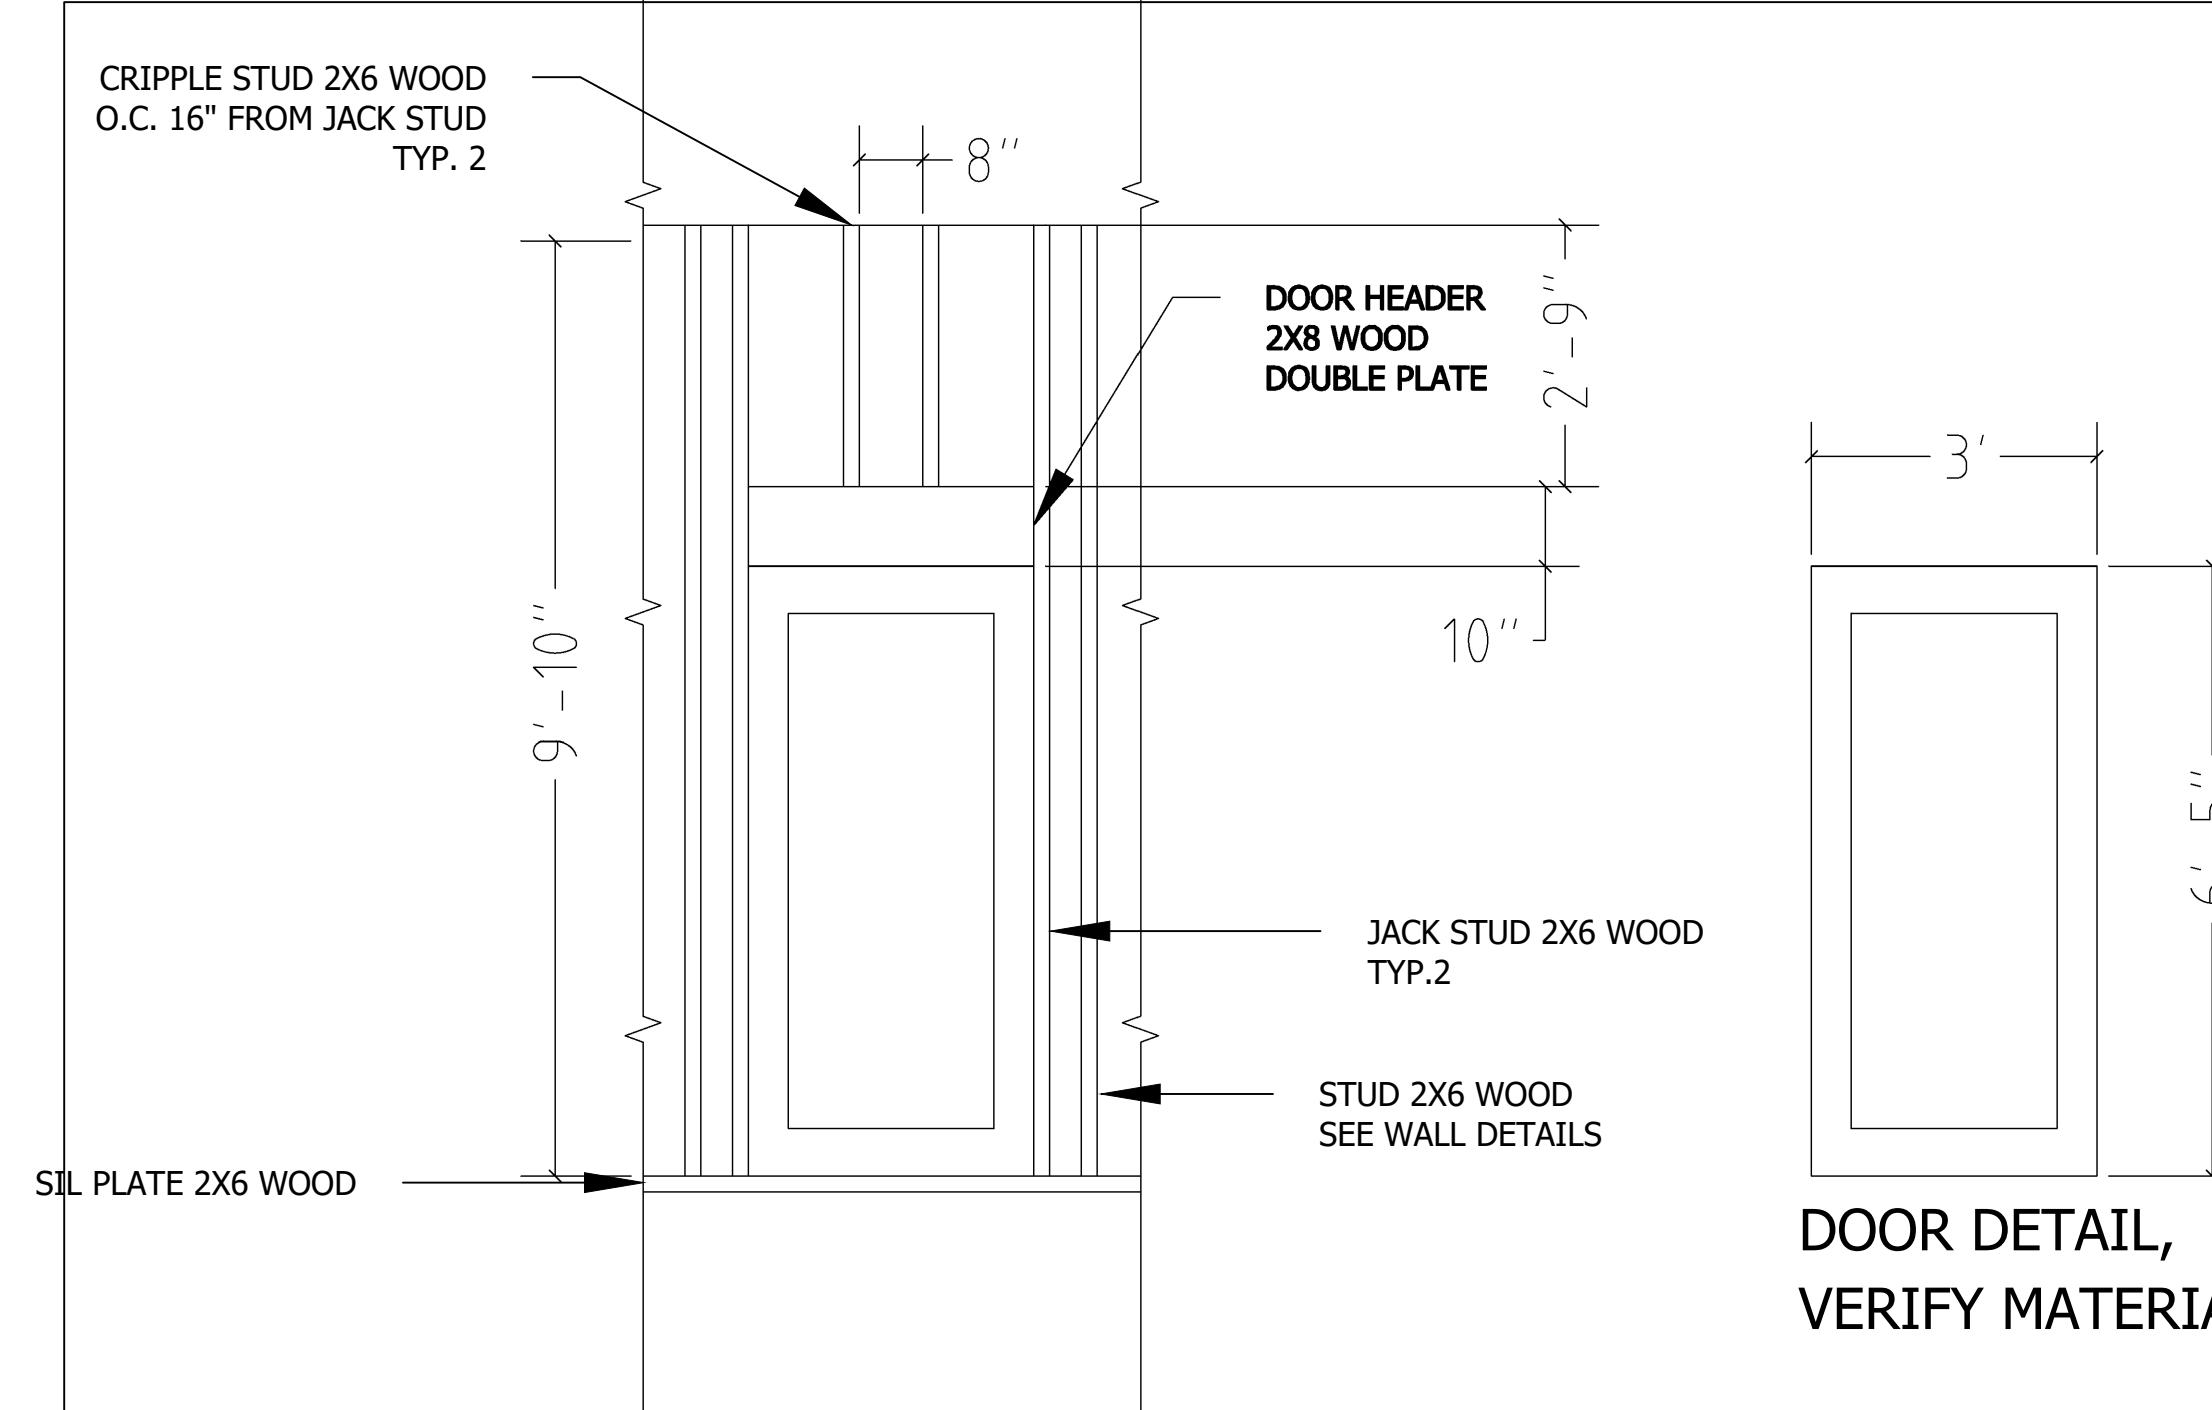


DOOR DETAIL

SCALE: 1/2"=1' 0"

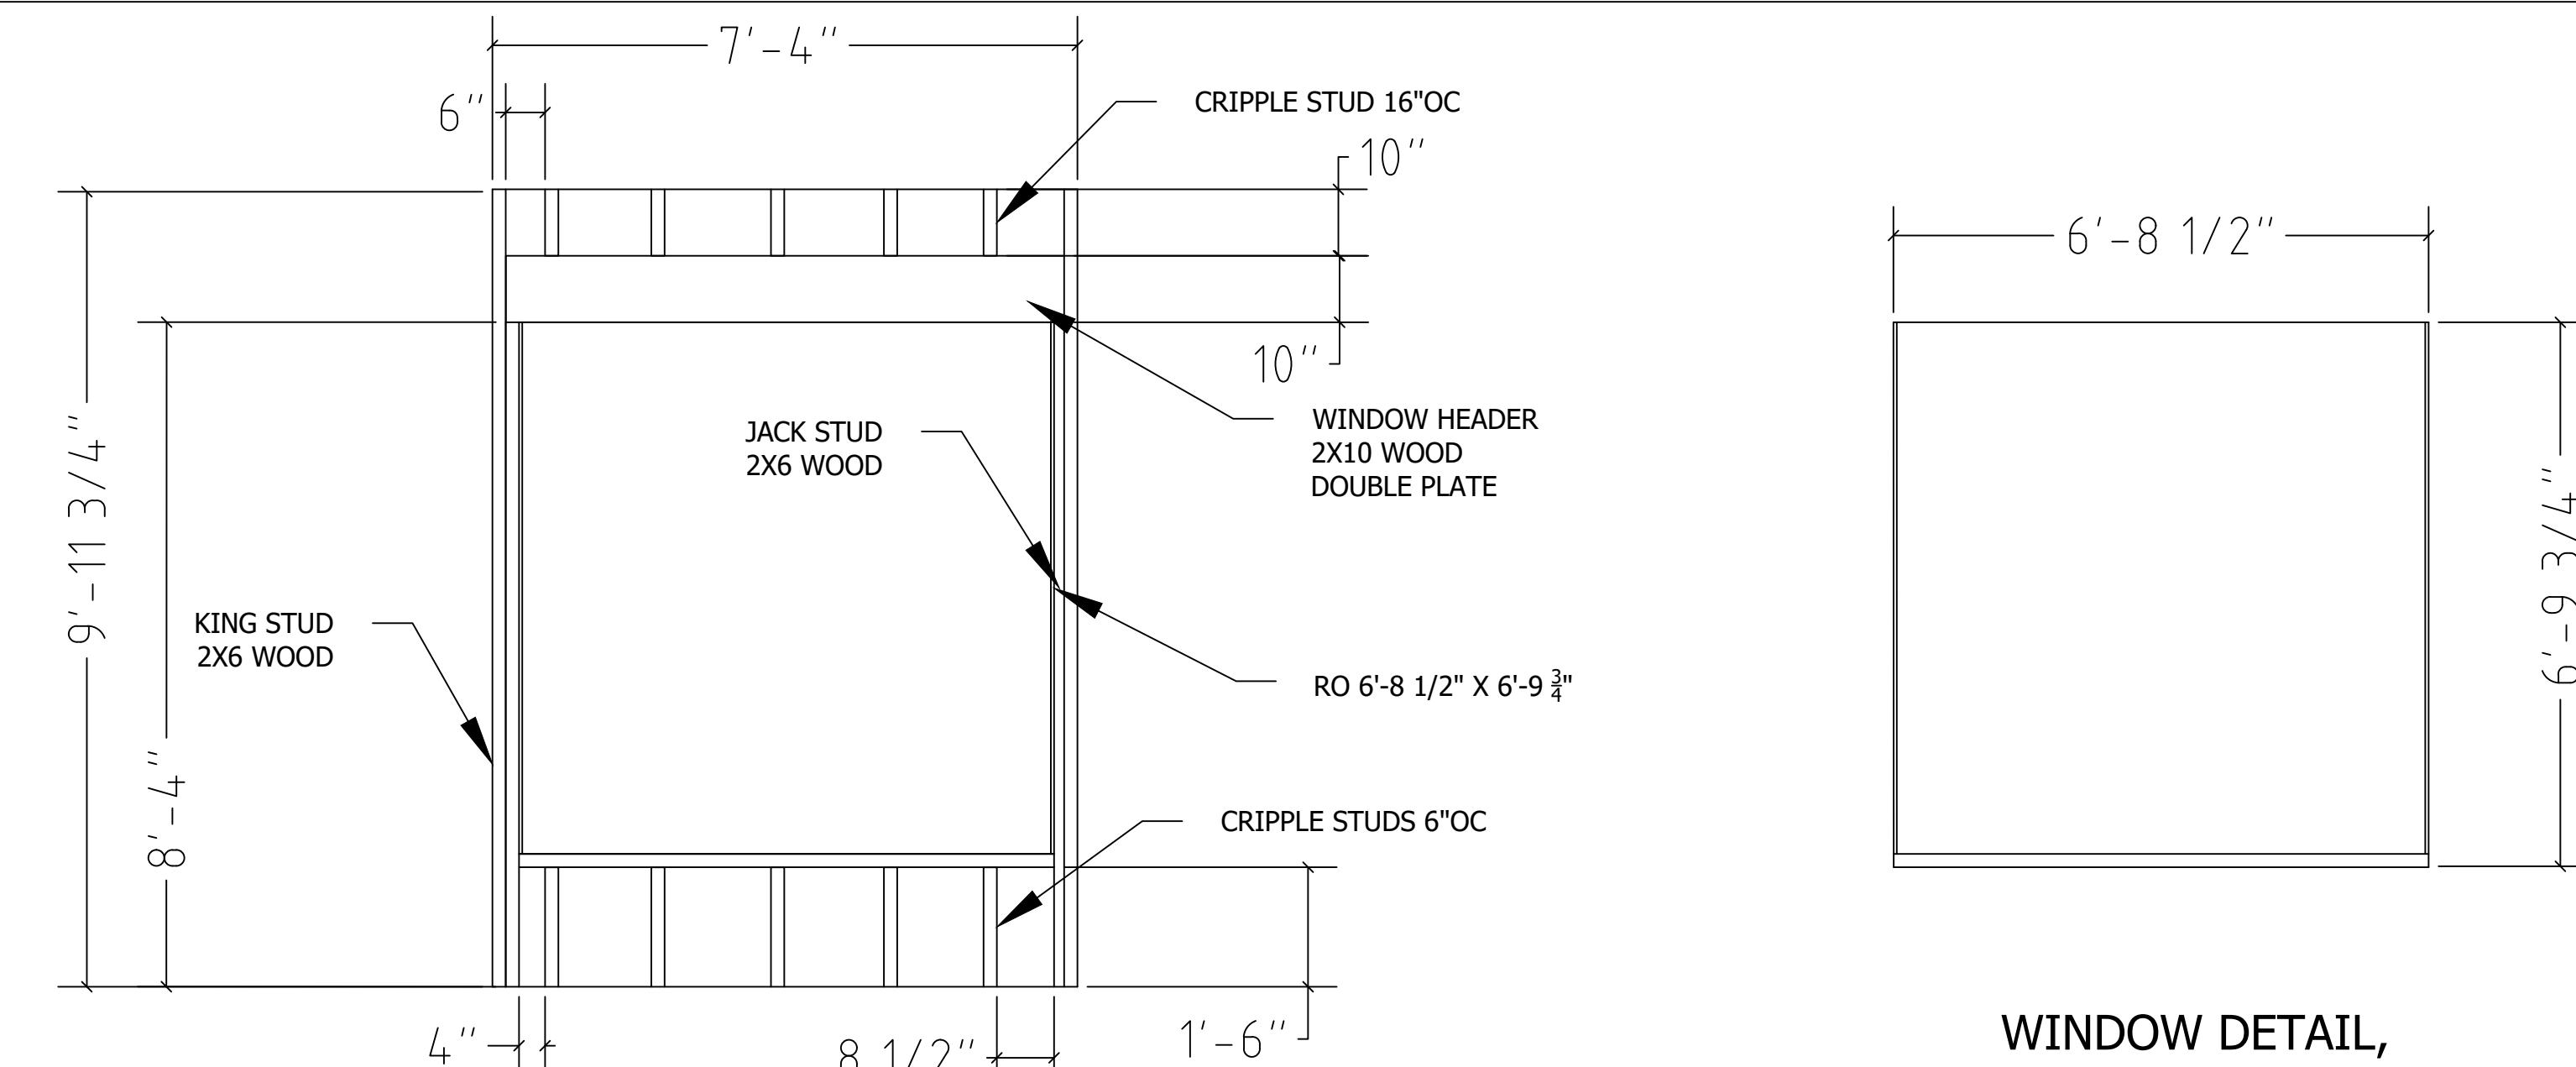

WINDOW DETAIL


SCALE: 1/2"=1' 0"

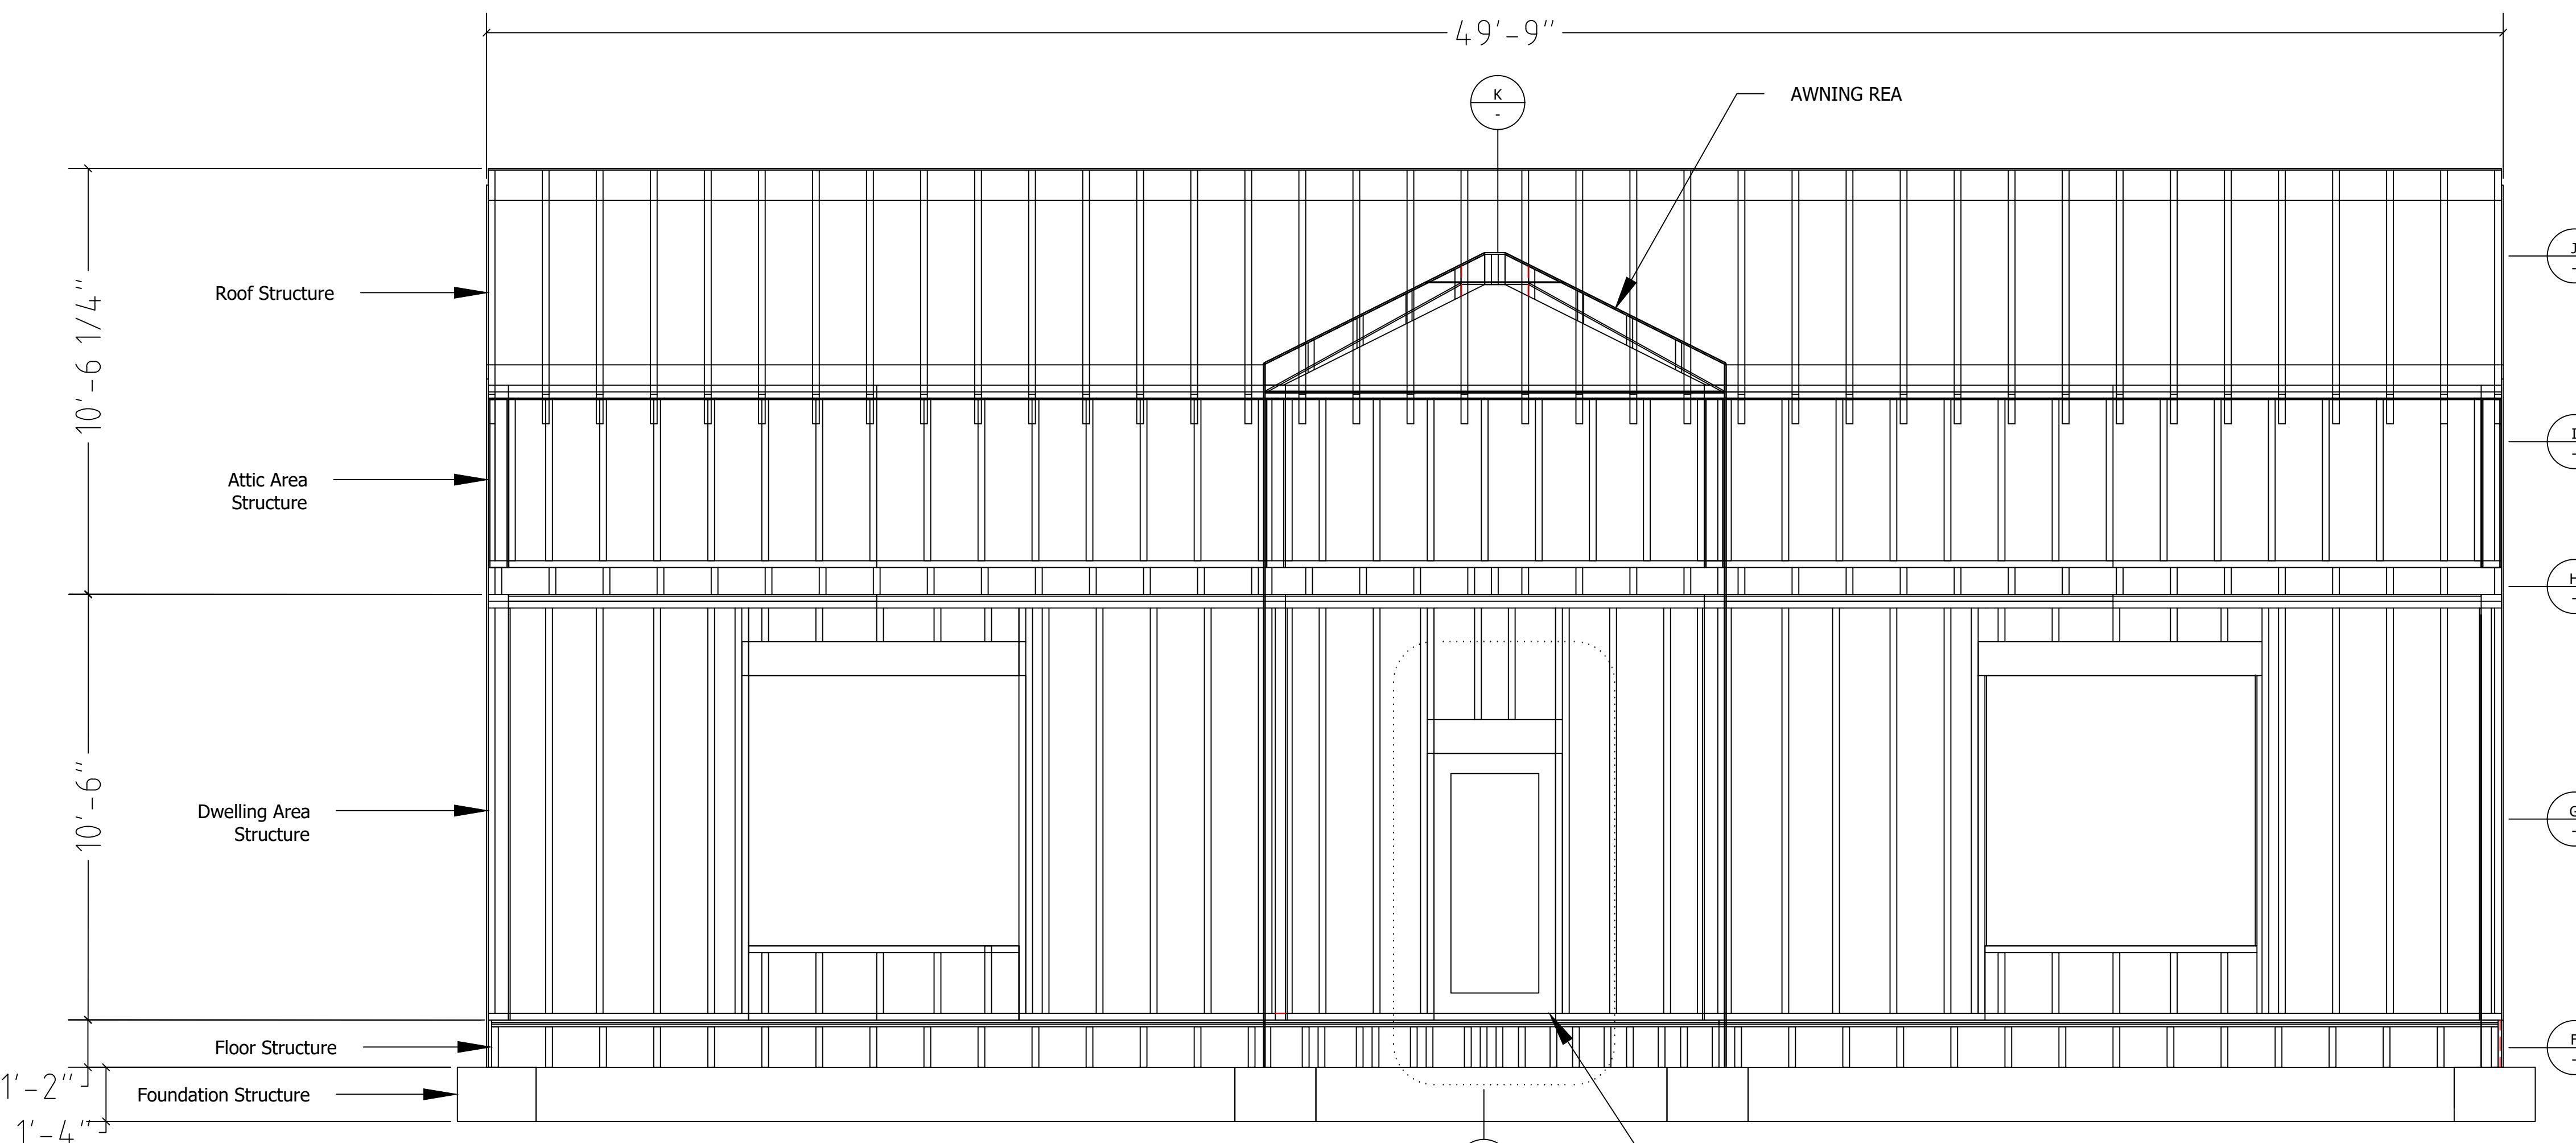


ELEVATION VIEW

SCALE: 3/8"=1' 0"

No.	Revision/Issue	Date
NDC		
CREATED BY NICK CORONA		
NEW HOUSE		
ADDRESS LOCATION		
PROJECT #	0000001	
DATE	03/31/2025	
ISSUE	BUILDING CONSENT	
DRAWING TITLE: STRUCTURAL SHEET: S05 DRAWING TITLE:		

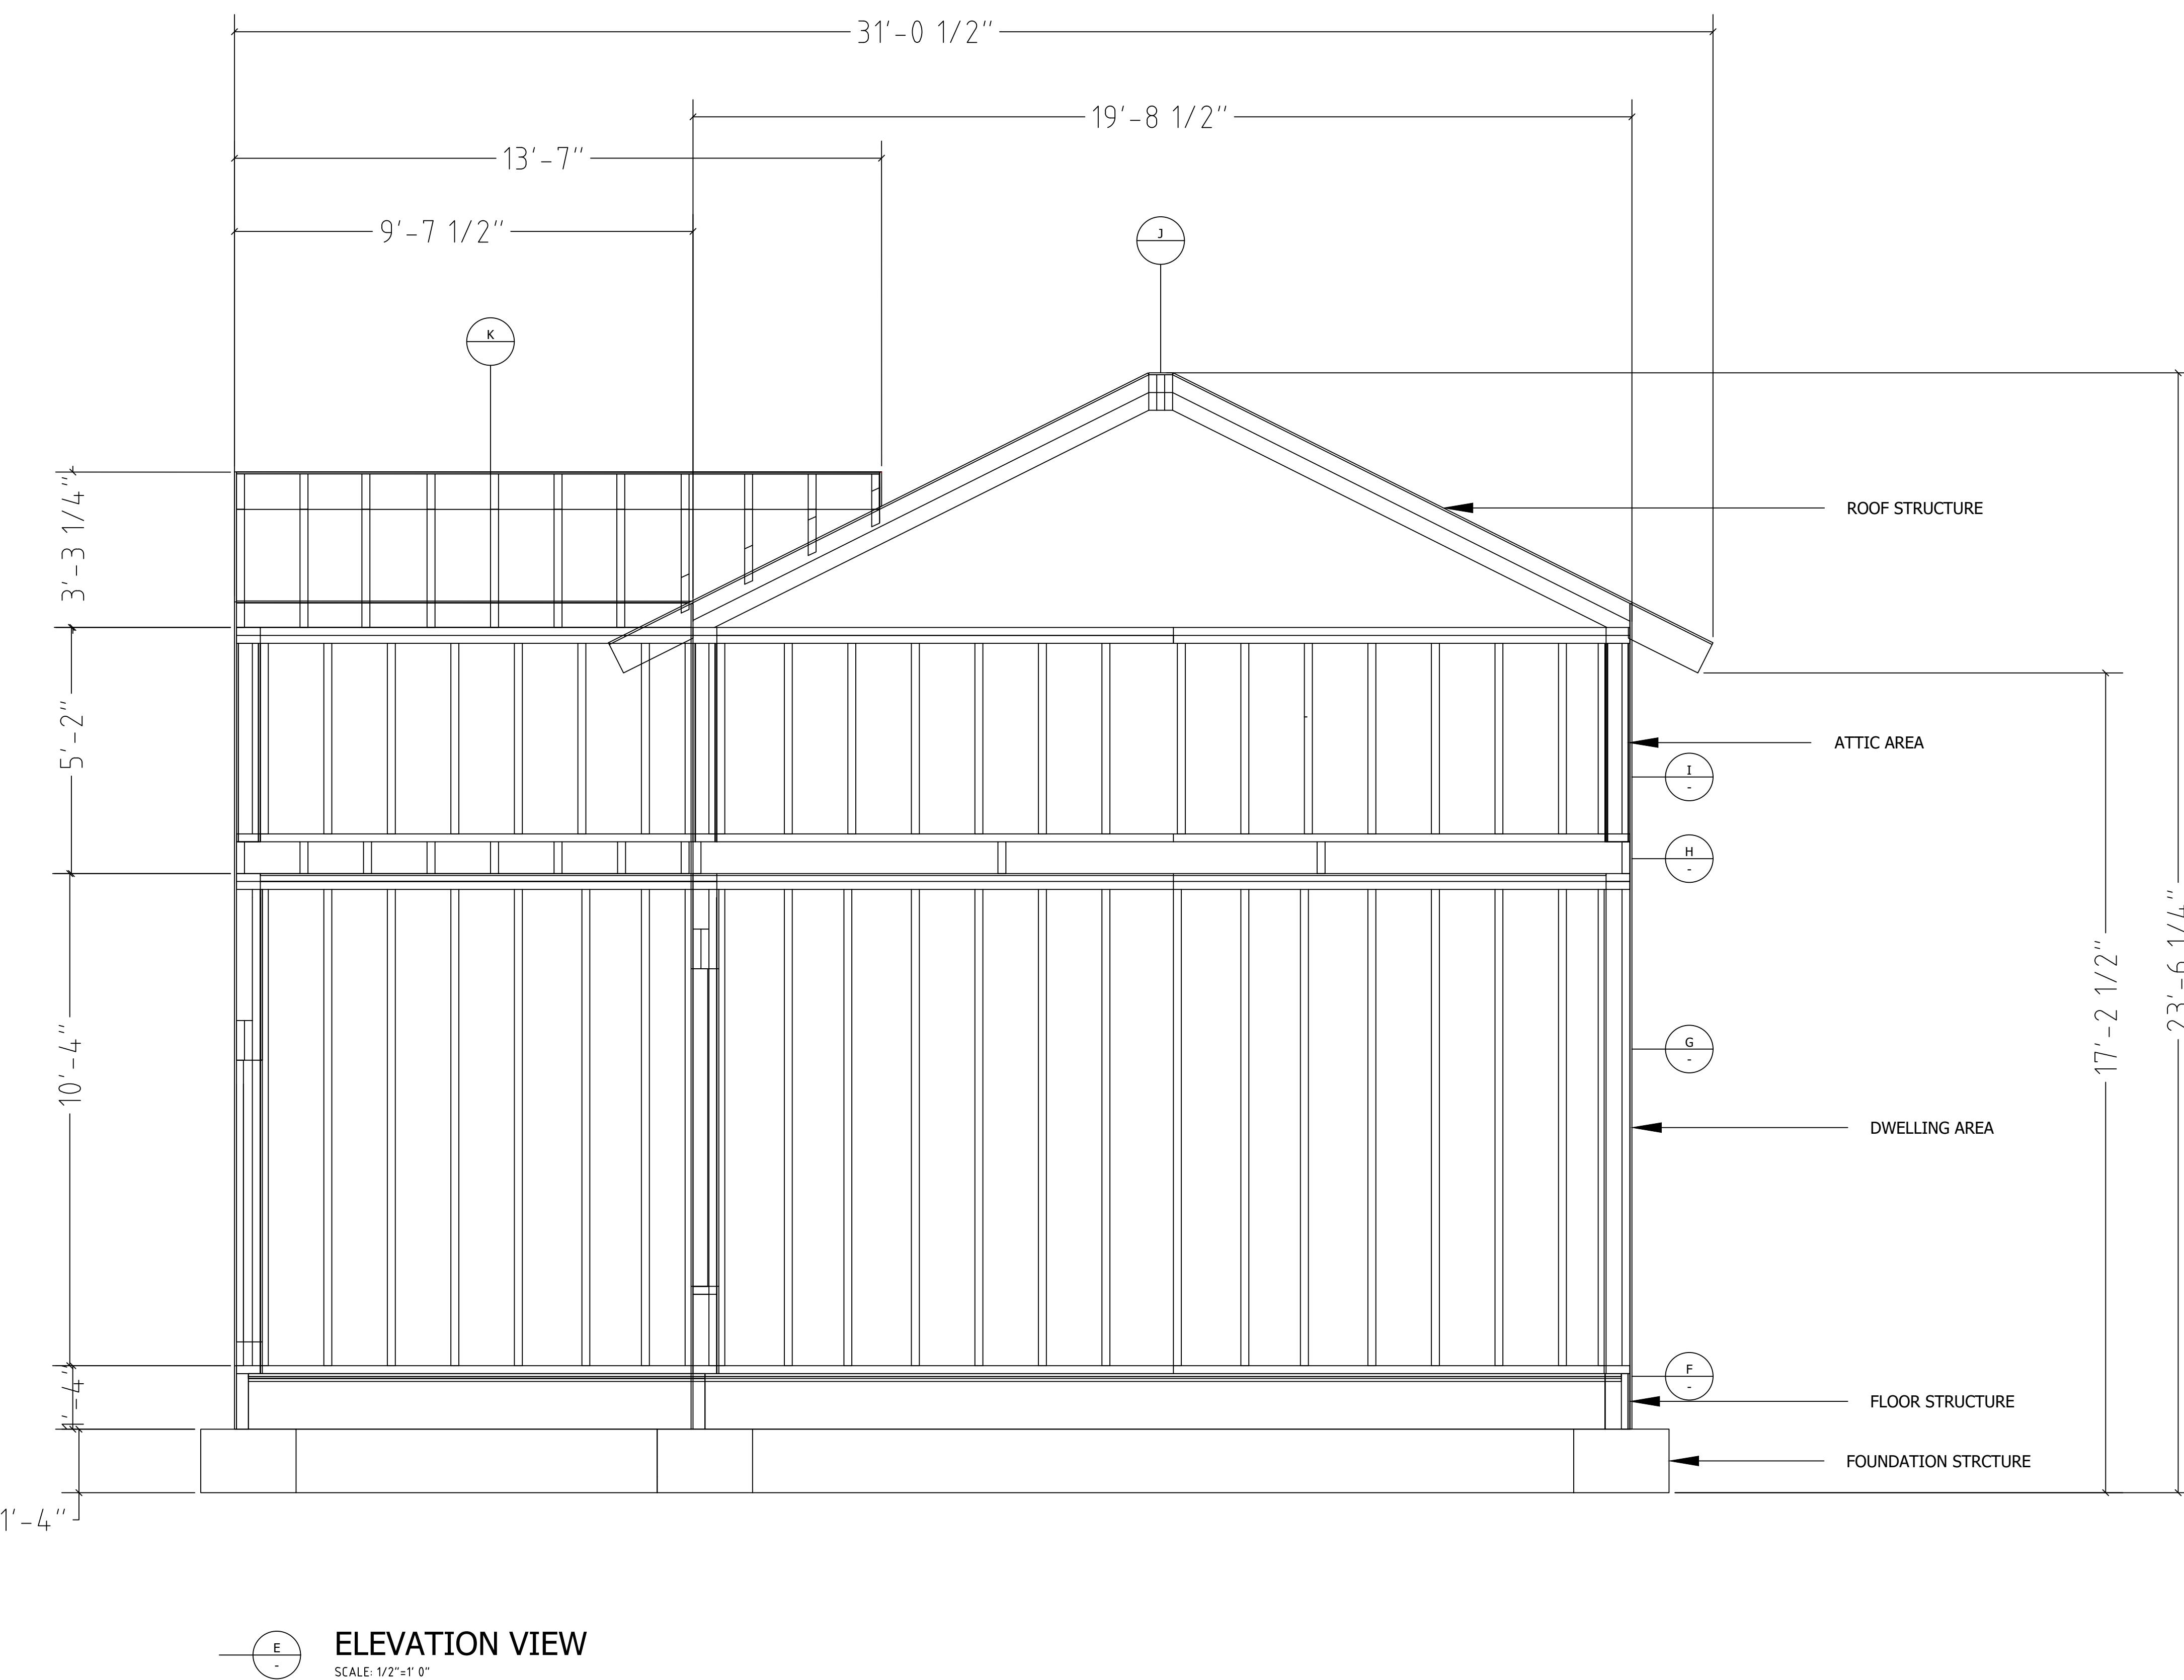


No	Revision/Issue	Date
 CREATED BY NICK CORONA		
NEW HOUSE		
ADDRESS LOCATION		
PROJECT #	0000001	
SHEET SIZE	A1	
DATE	03/31/2025	
ISSUE	BUILDING CONSENT	
STRUCTURAL		
SHEET:	DRAWING TITLE: S06	

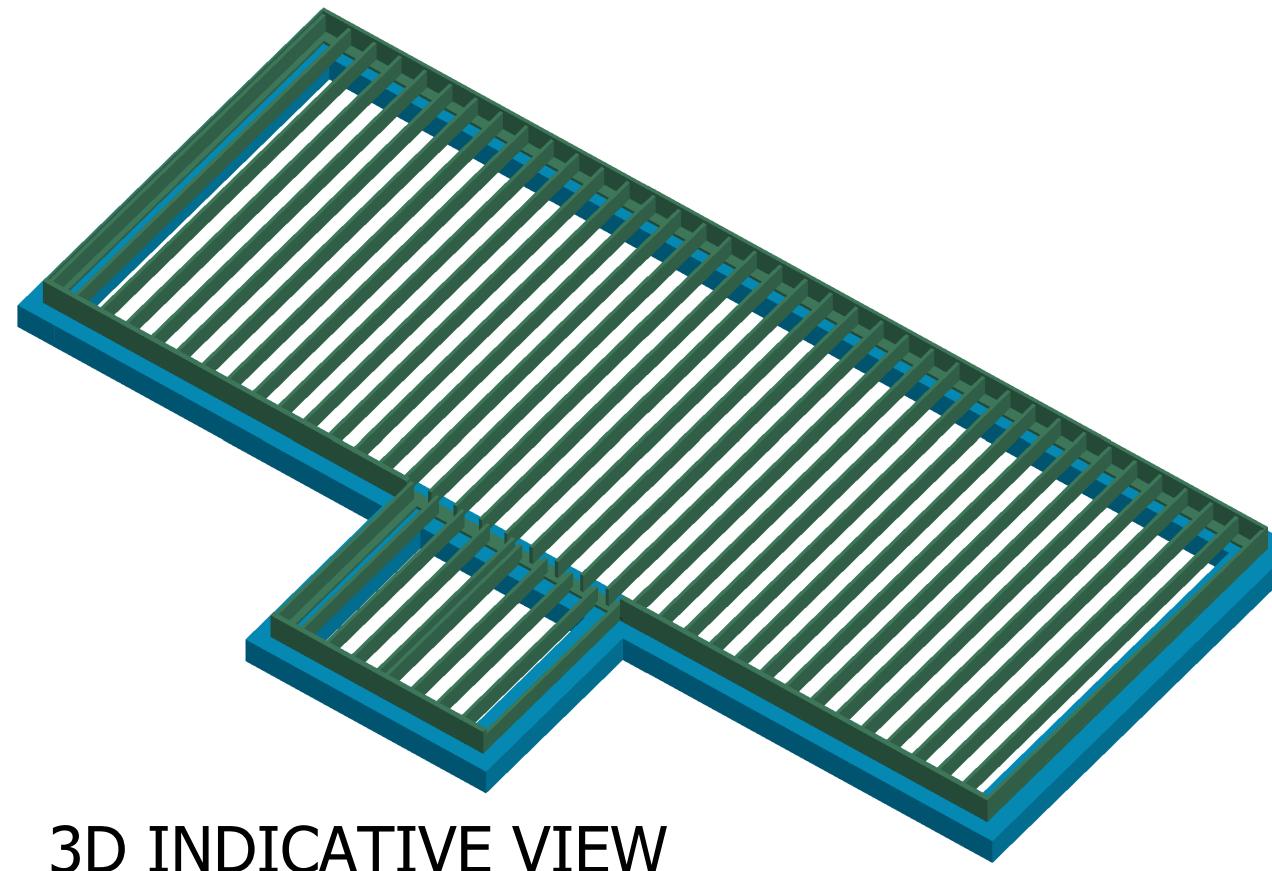

3D INDICATIVE VIEW

AWNING FLOOR JOIST
2X10 WOOD 16" OC
8'-11" LENGTH
FASTEN TO SIL PLATE

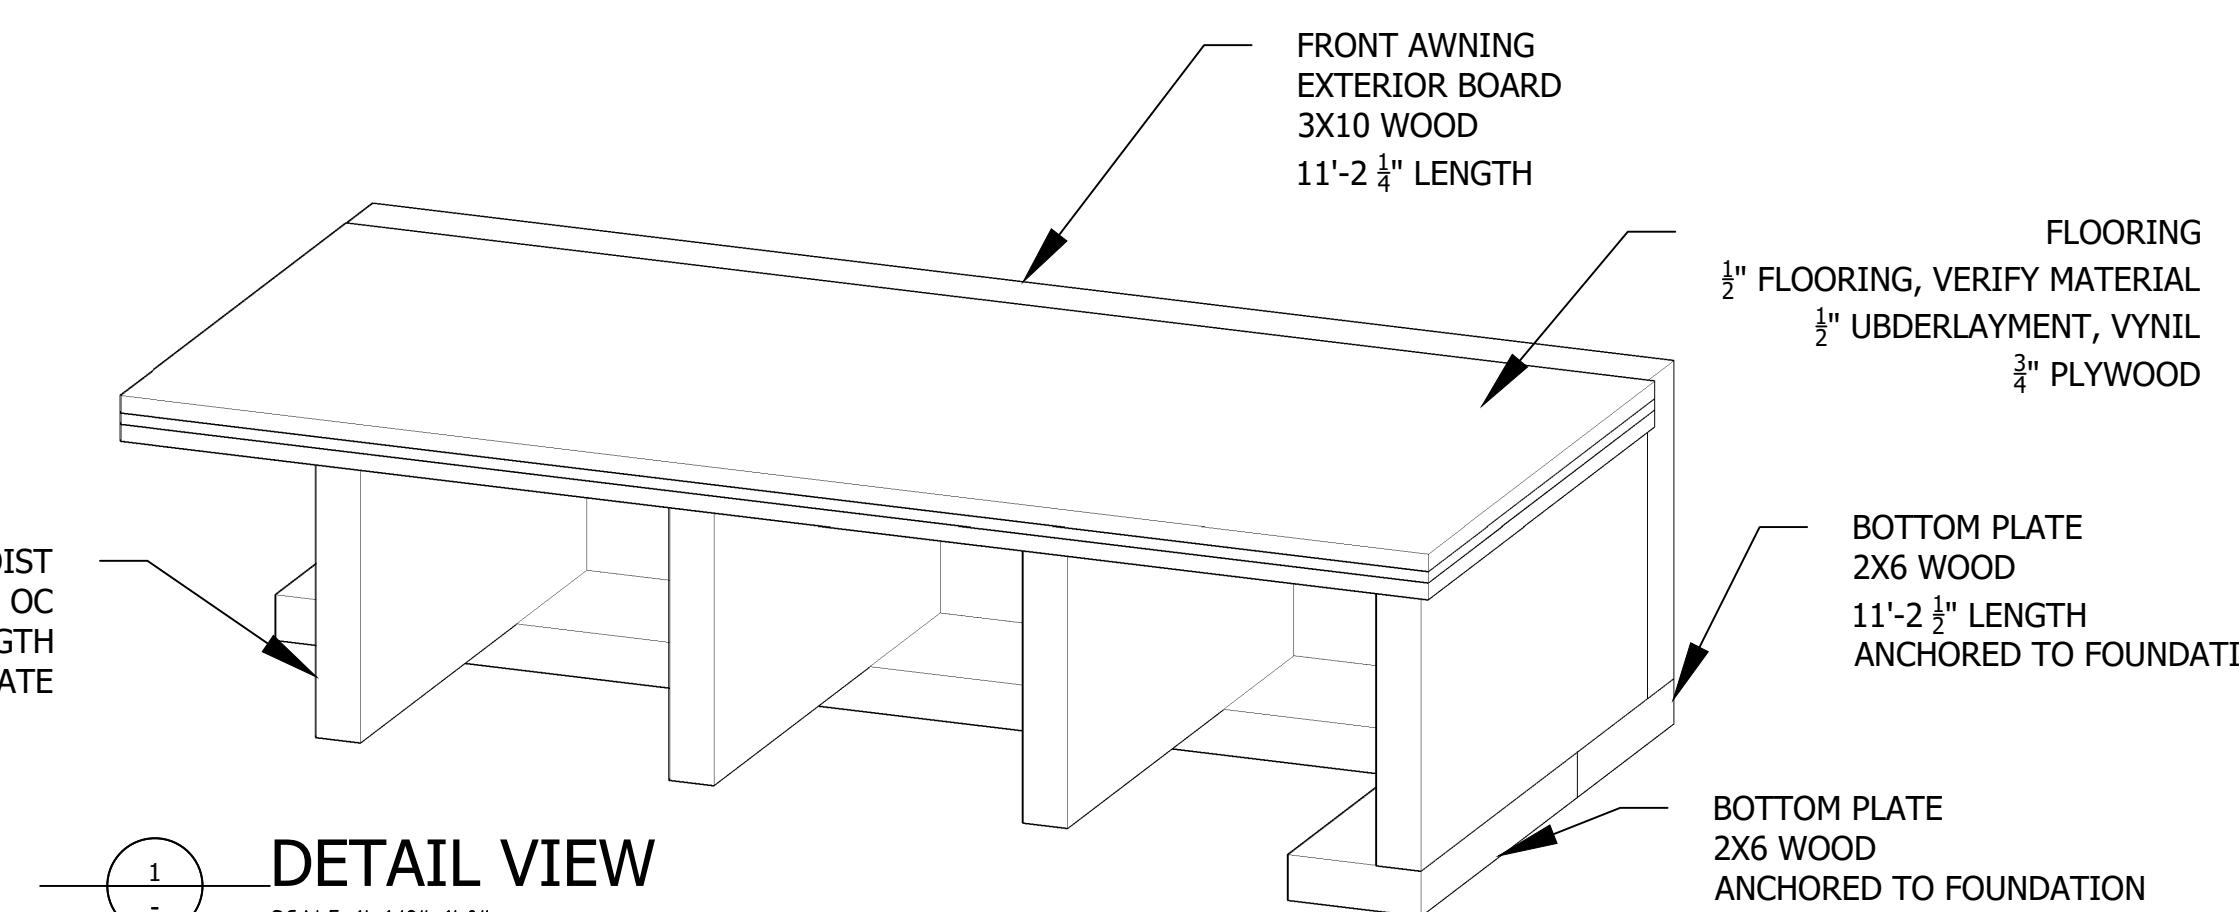

DETAIL VIEW
SCALE: 1'-1/2"=1' 0"


FRONT AWNING
EXTERIOR BOARD
3X10 WOOD
11'-2 1/4" LENGTH

FLOORING
1/2" FLOORING, VERIFY MATERIAL
1/2" UNDERLAYMENT, VINYL
3/4" PLYWOOD

BOTTOM PLATE
2X6 WOOD
11'-2 1/4" LENGTH
ANCHORED TO FOUNDATION


BOTTOM PLATE
2X6 WOOD
ANCHORED TO FOUNDATION

EXTERIOR BOARD
2X10 WOOD
49'-7 3/4" LENGTH


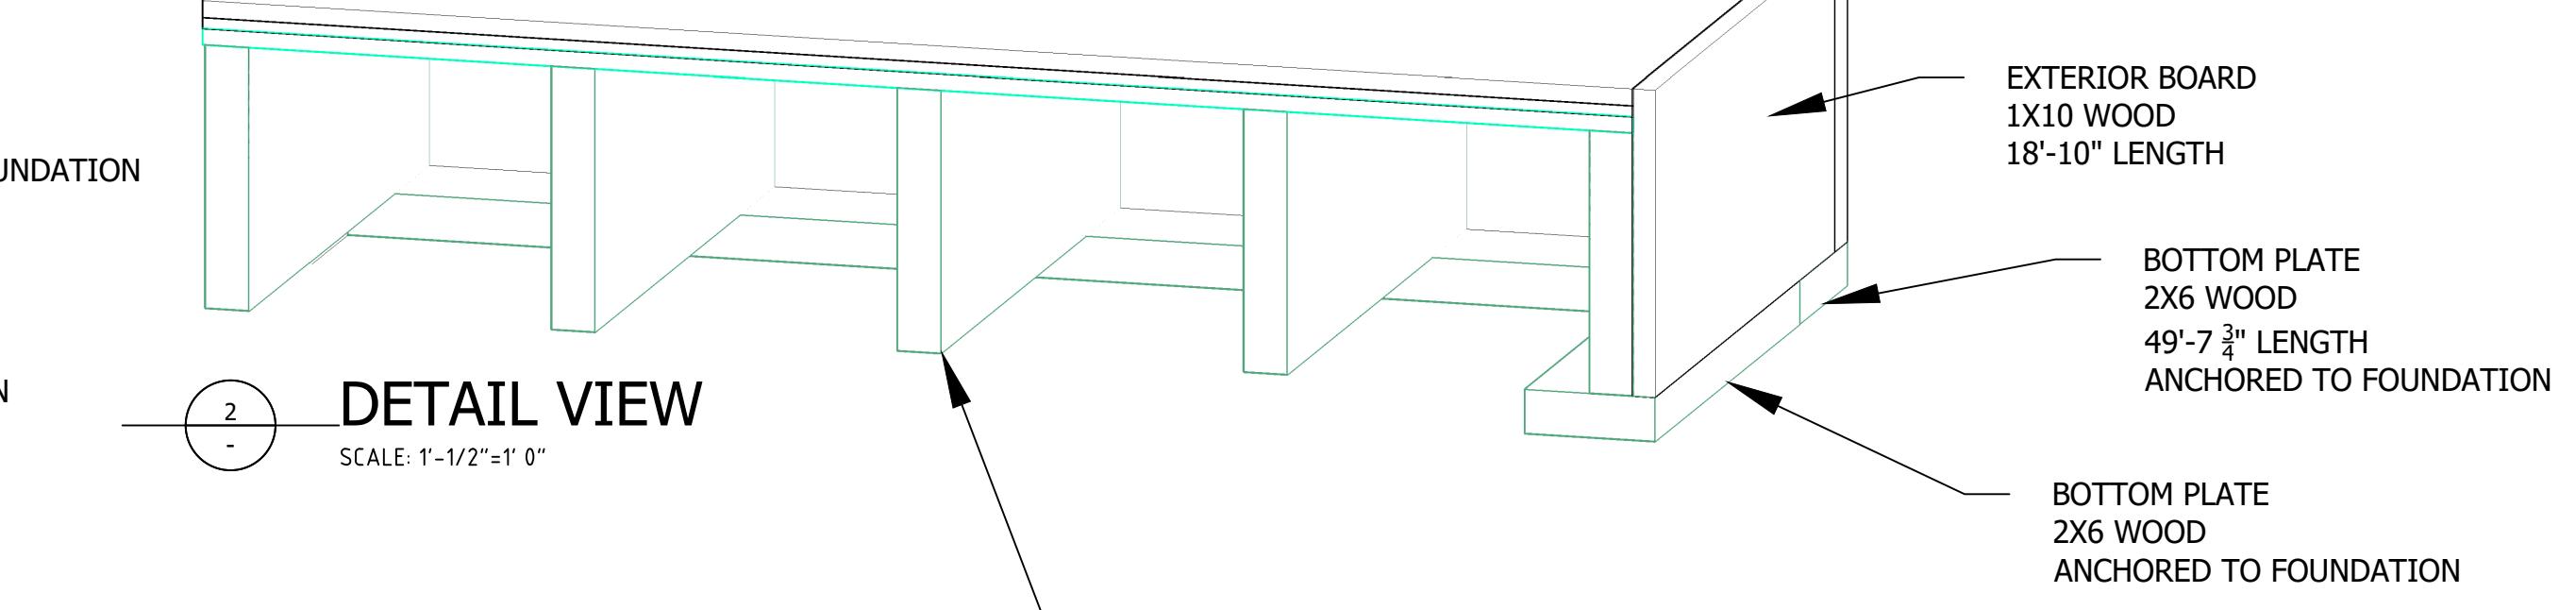


DETAIL VIEW
SCALE: 1'-1/2"=1' 0"


FLOOR JOIST
2X10 WOOD 16" OC
19'-2 15/16" LENGTH
FASTEN TO SIL PLATE

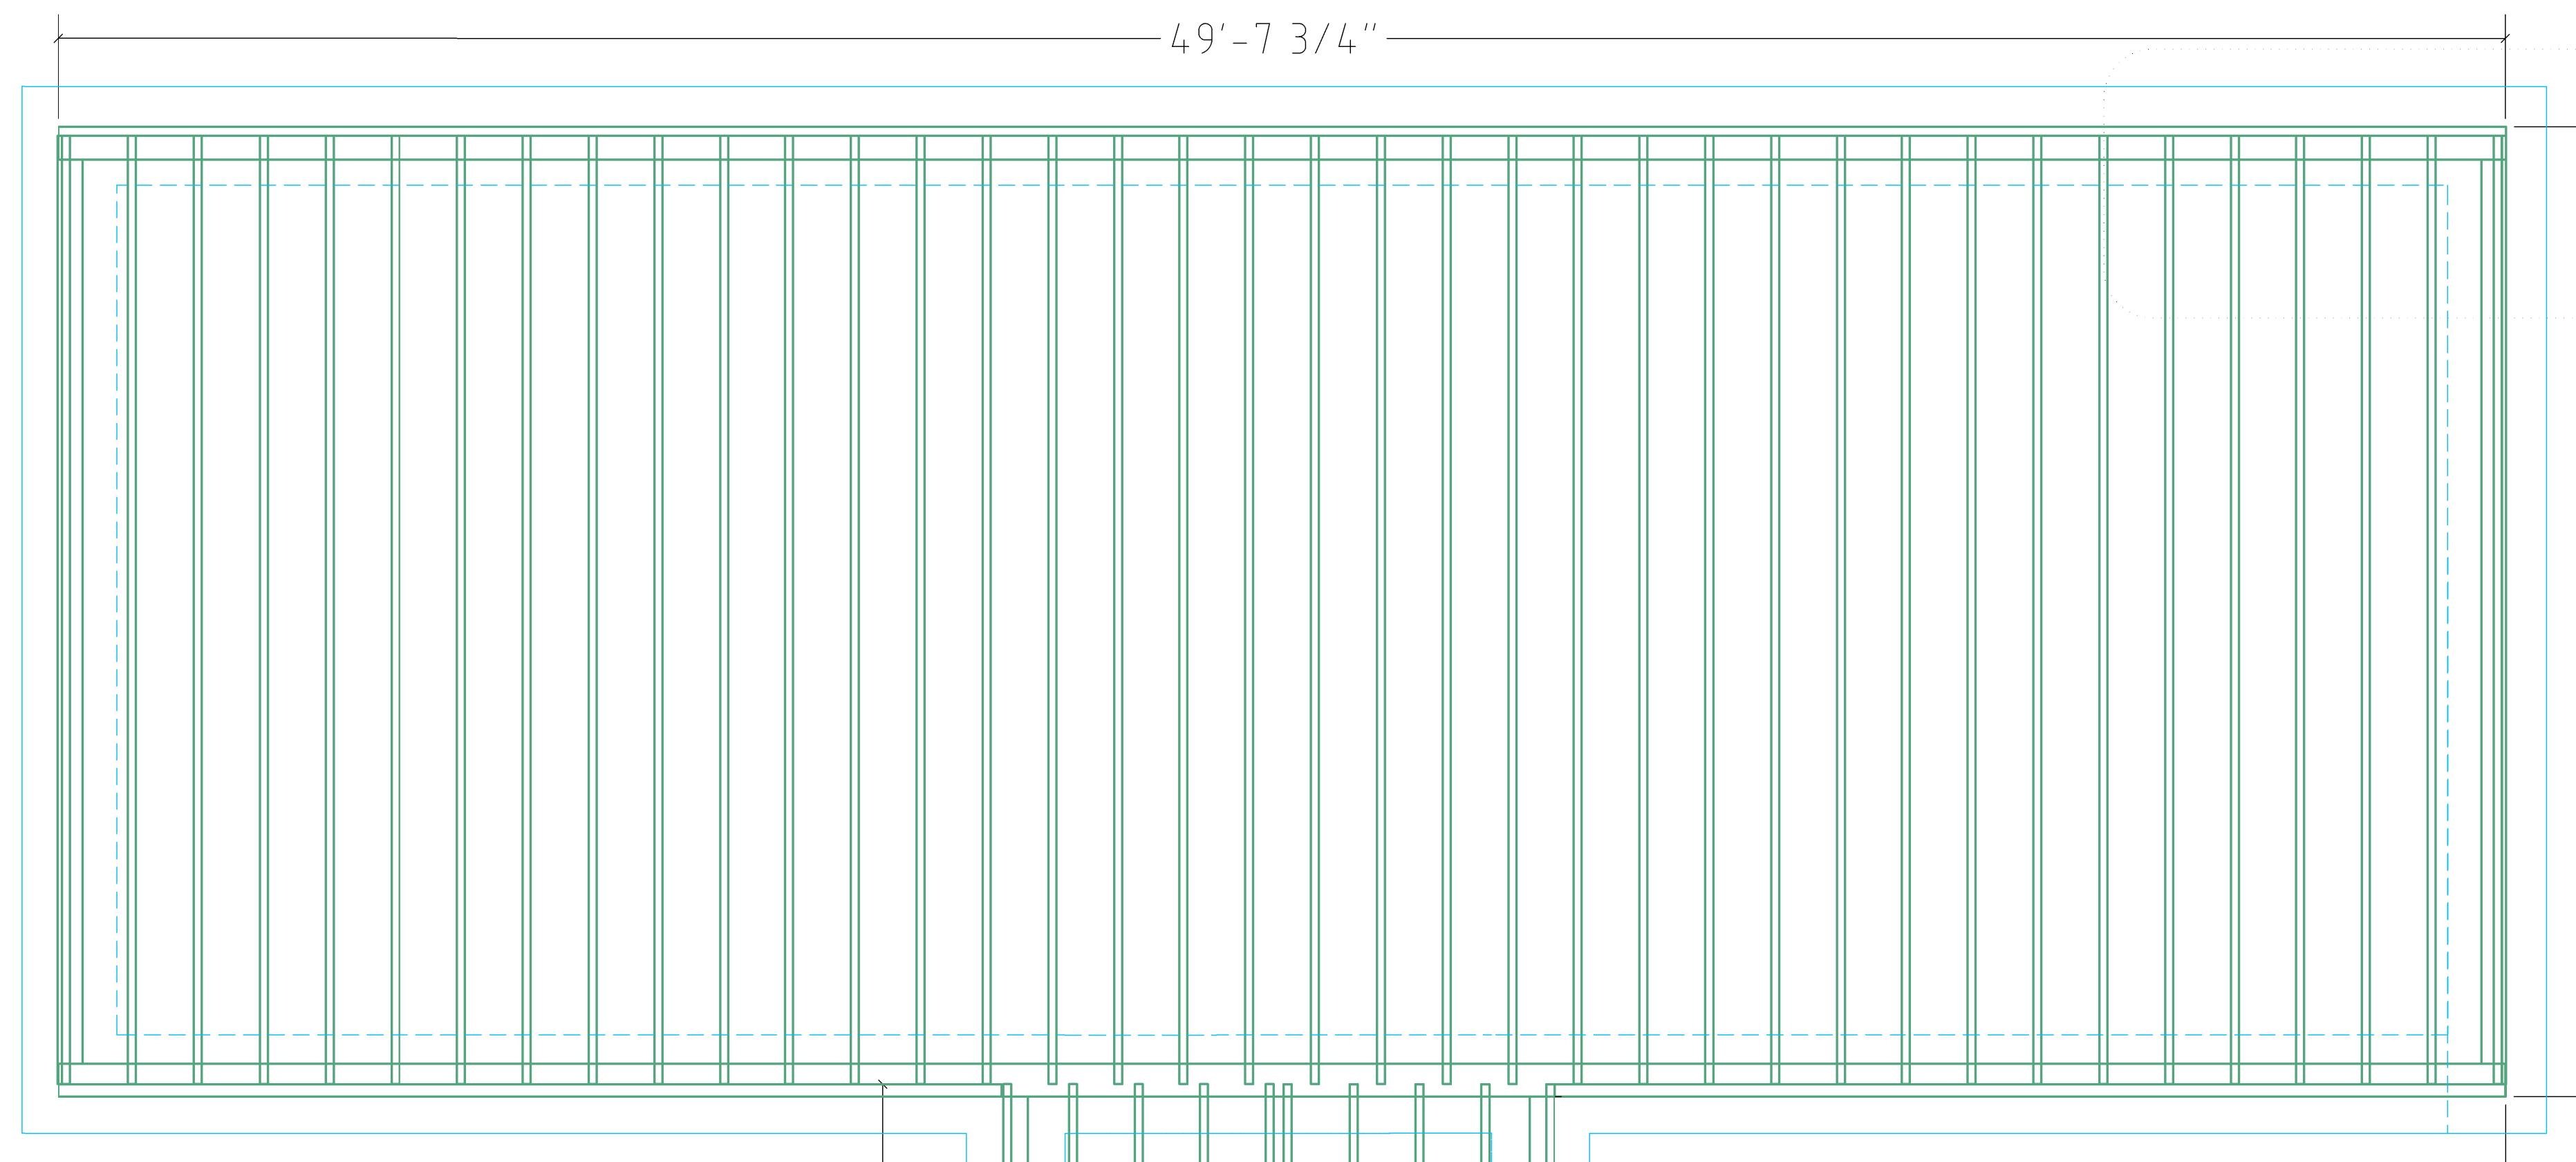



No.	Revision/Issue	Date
NDC CREATED BY NICK CORONA		
NEW HOUSE		
ADDRESS LOCATION		
PROJECT # 0000001		
SHEET SIZE A1		
DATE 03/31/2025		
ISSUE BUILDING CONSENT		
DRAWING TITLE: STRUCTURAL		
SHEET: S07	DRAWING TITLE:	

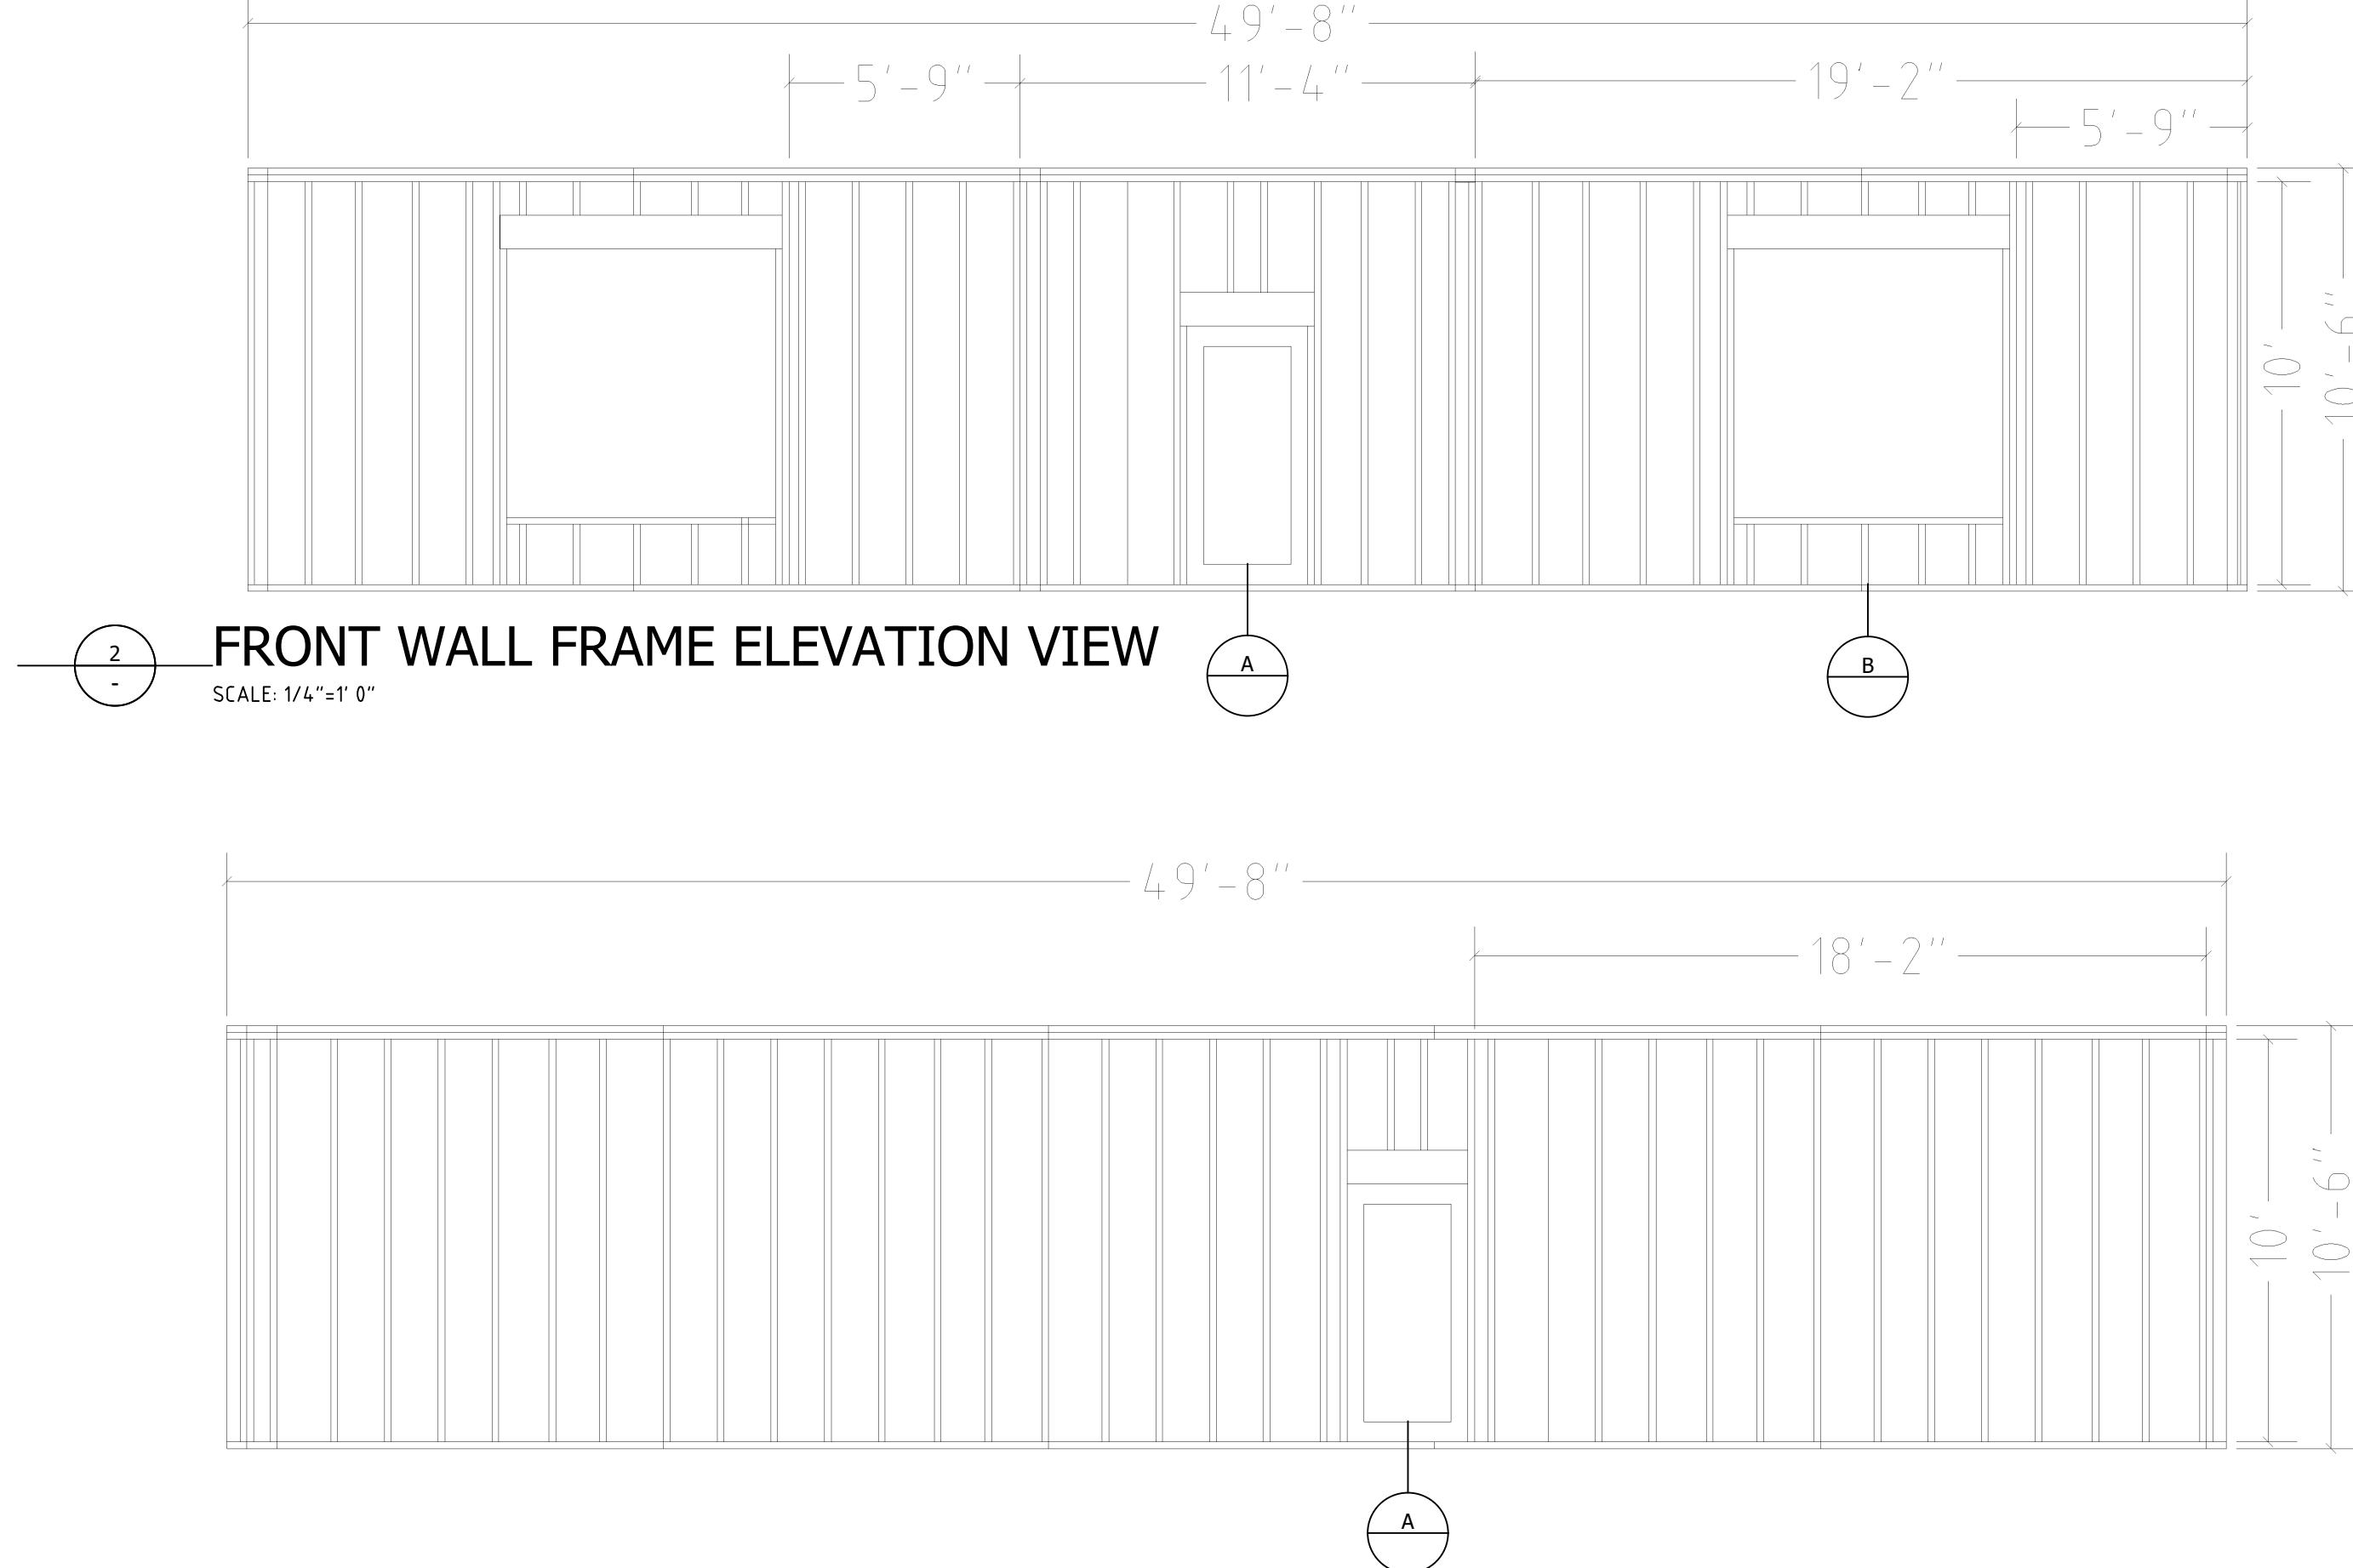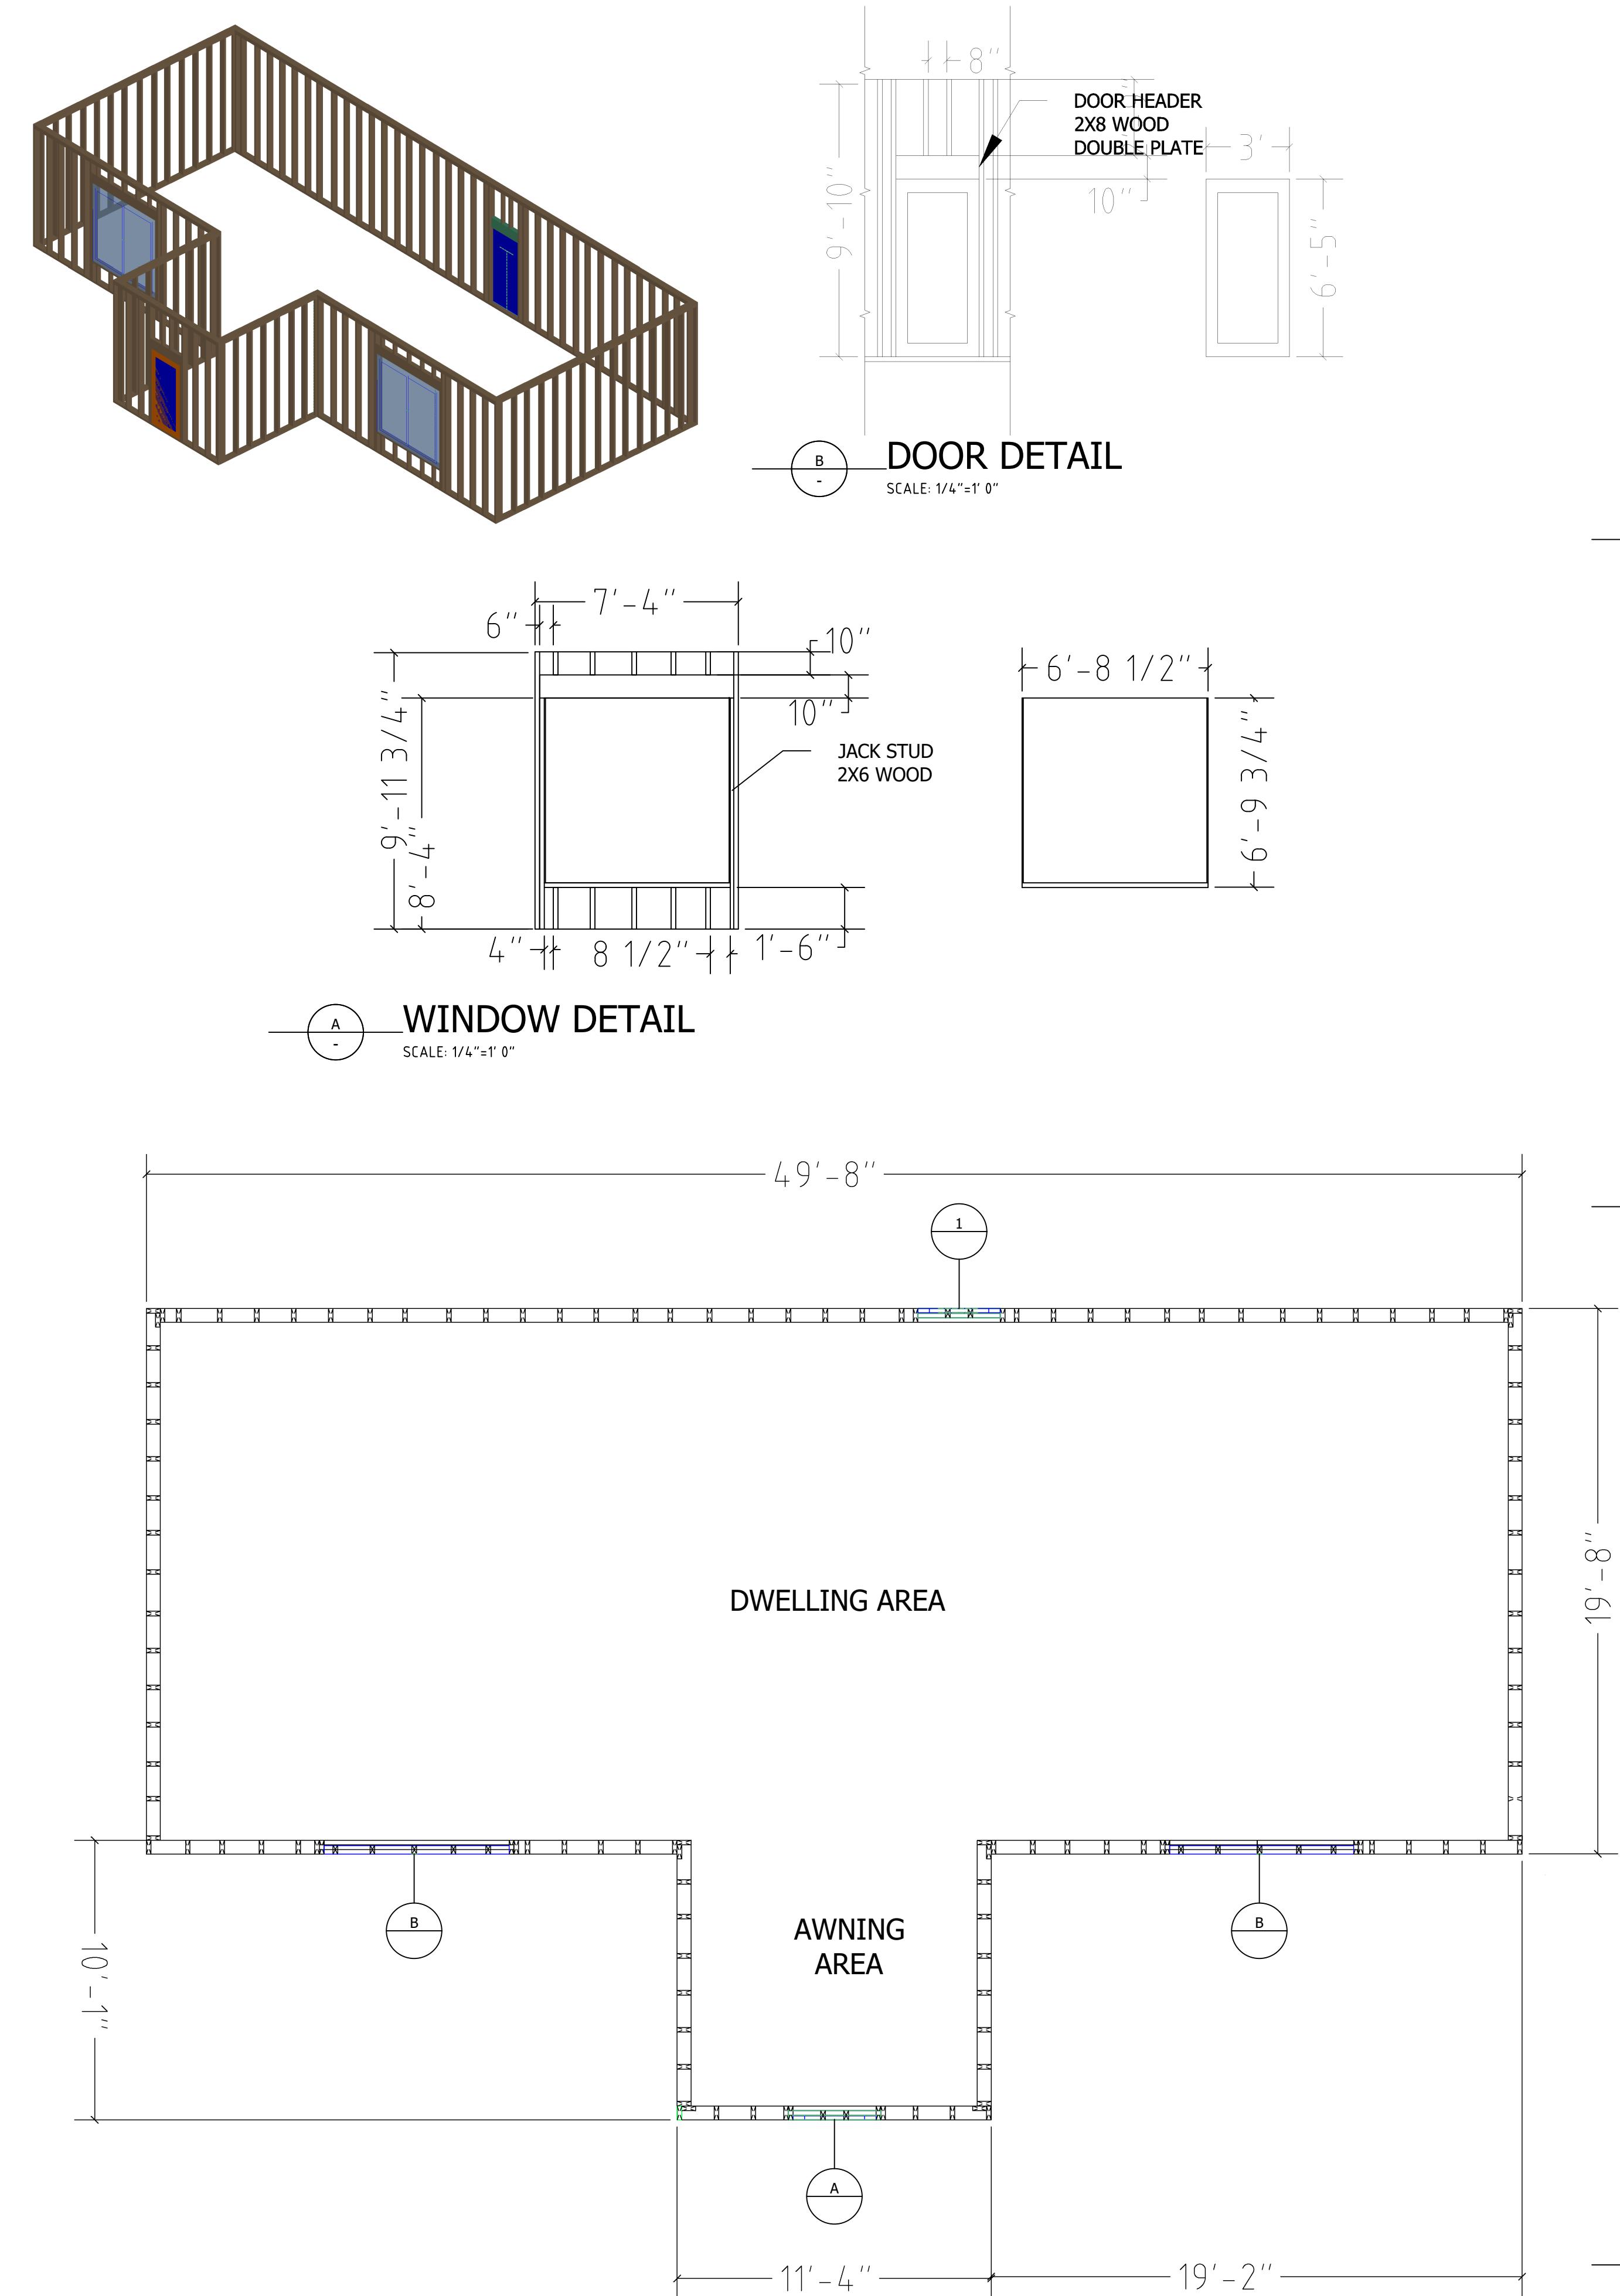



No.	Revision/Issue	Date
NDC CREATED BY NICK CORONA		
NEW HOUSE		
ADDRESS LOCATION		
PROJECT #	0000001	
SHEET SIZE	A1	
DATE	03/31/2025	
ISSUE	BUILDING CONSENT	
DRAWING TITLE:		
STRUCTURAL		
SHEET:	S08	
DRAWING TITLE:		

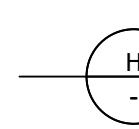
 ATTIC FLOOR STRUCTURE
SCALE: 3/8"=1' 0"


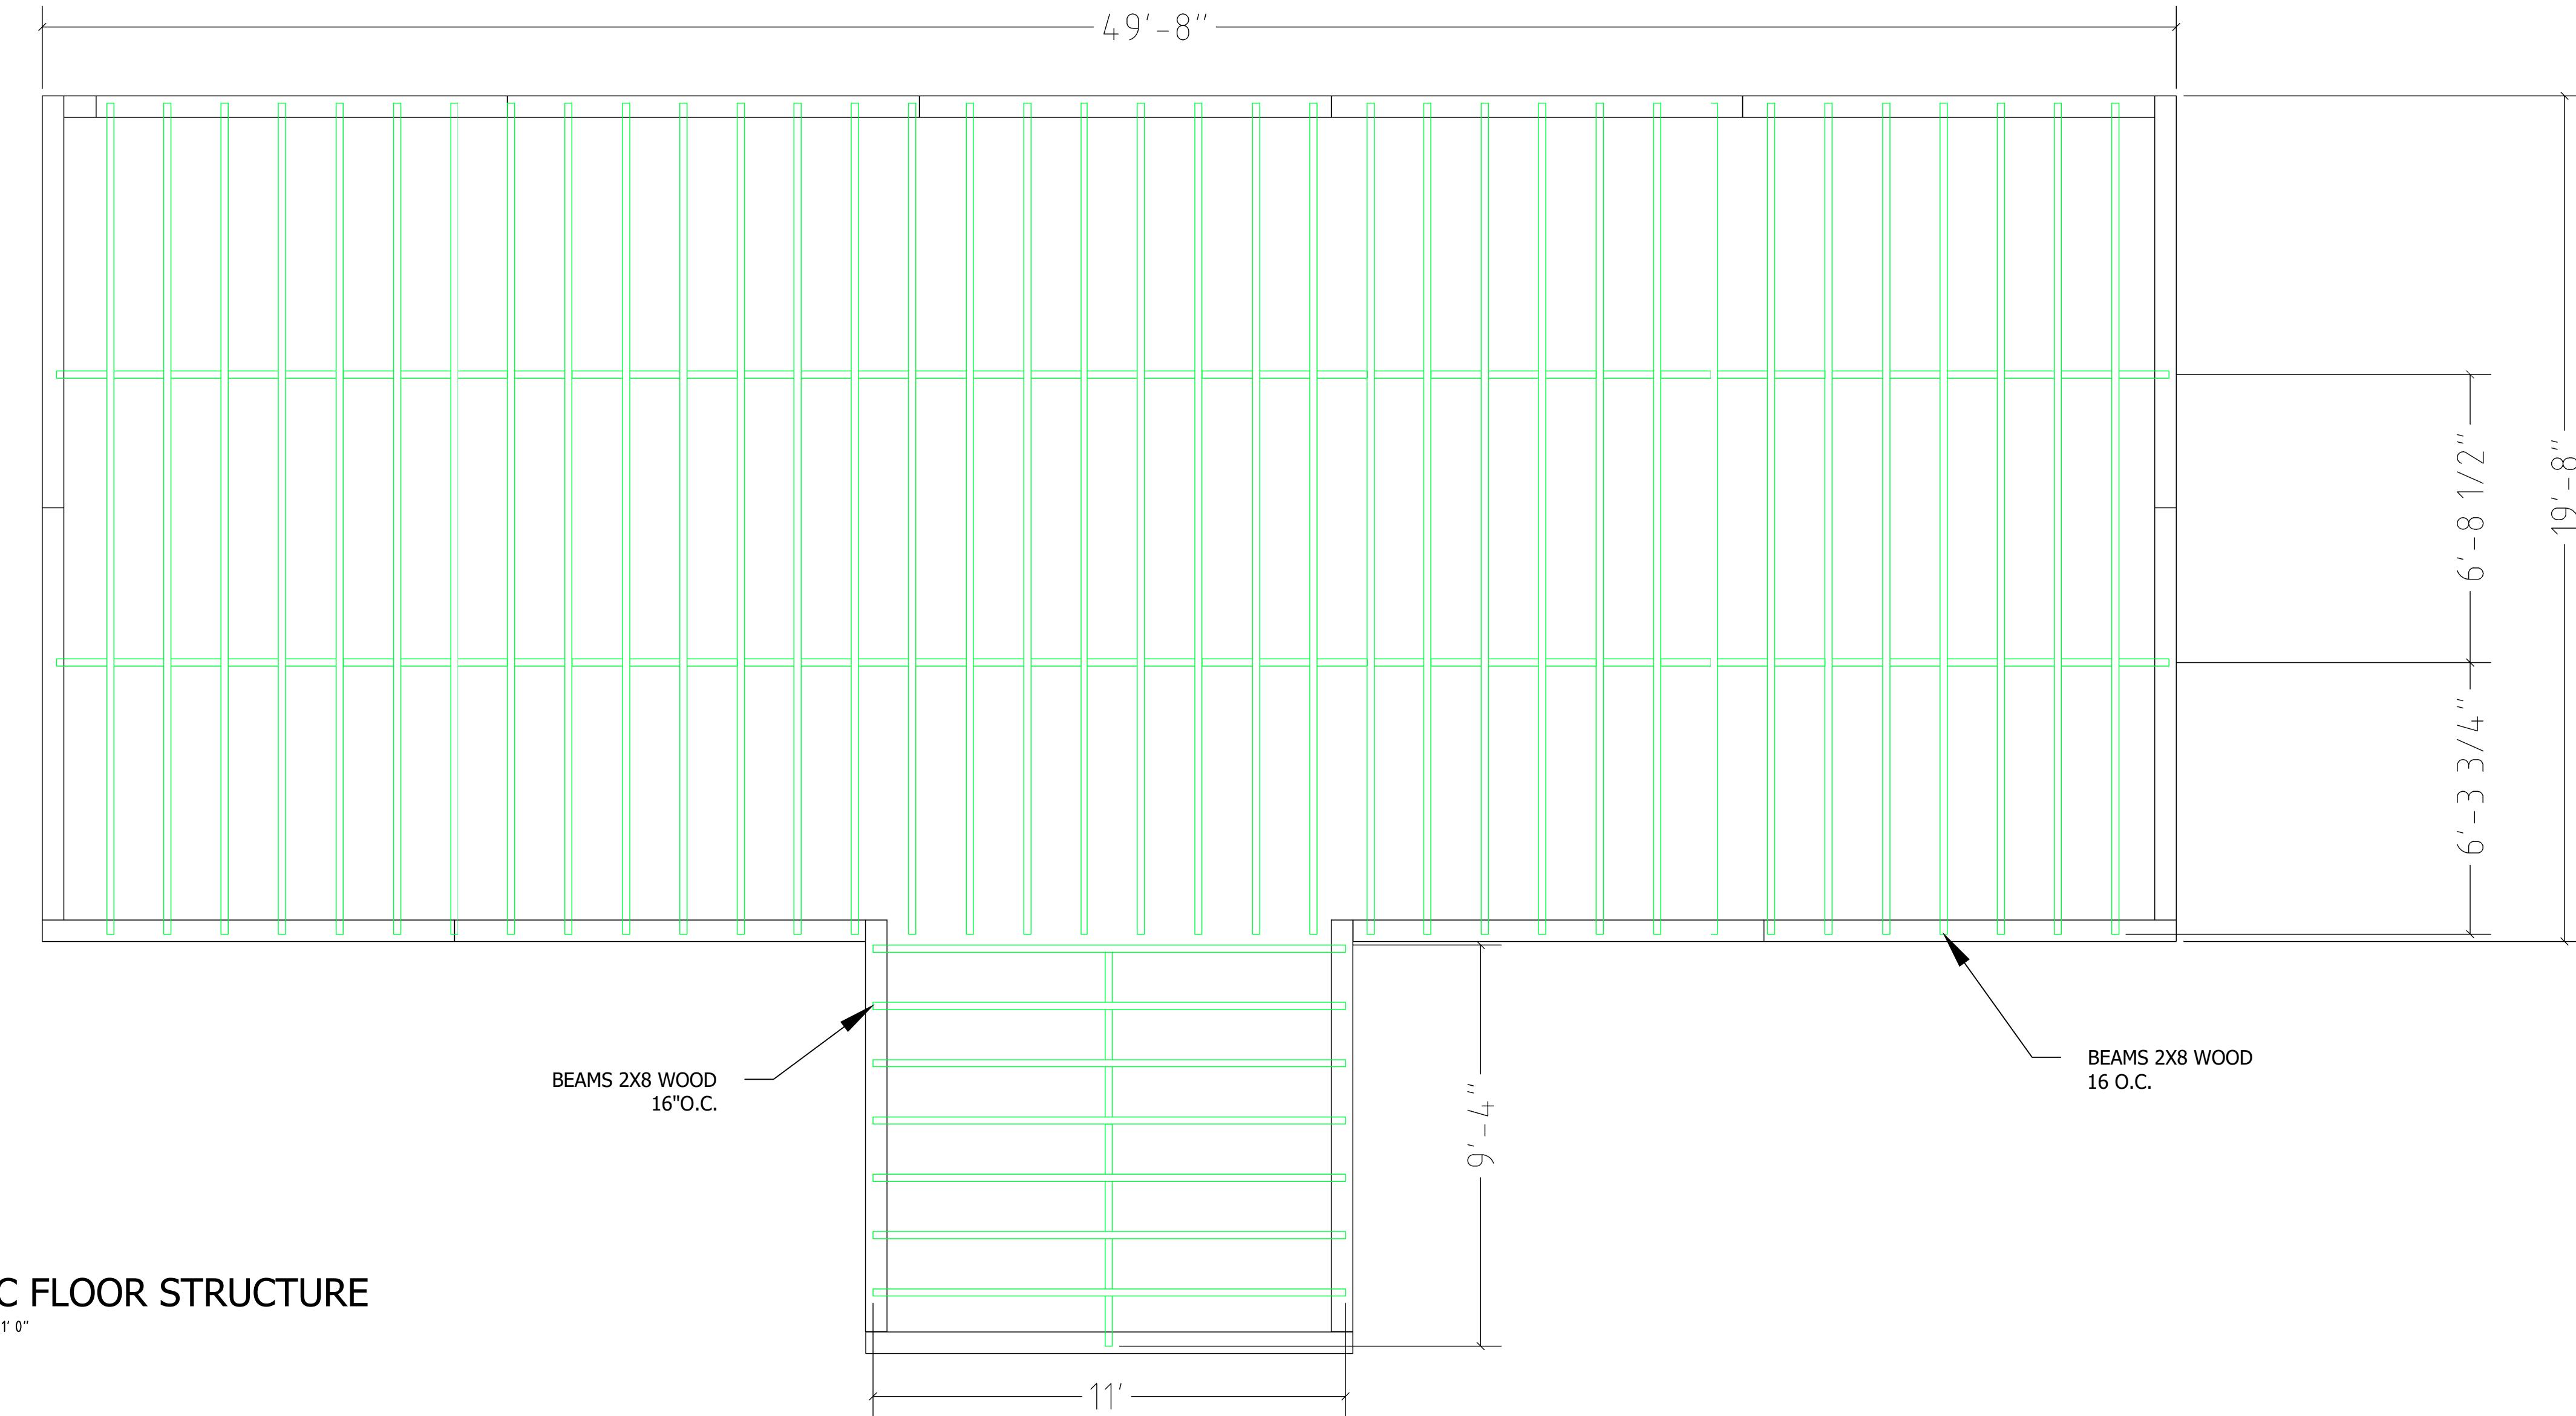


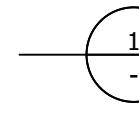 3D INDICATIVE IMAGE
SCALE: 3/8"=1' 0"

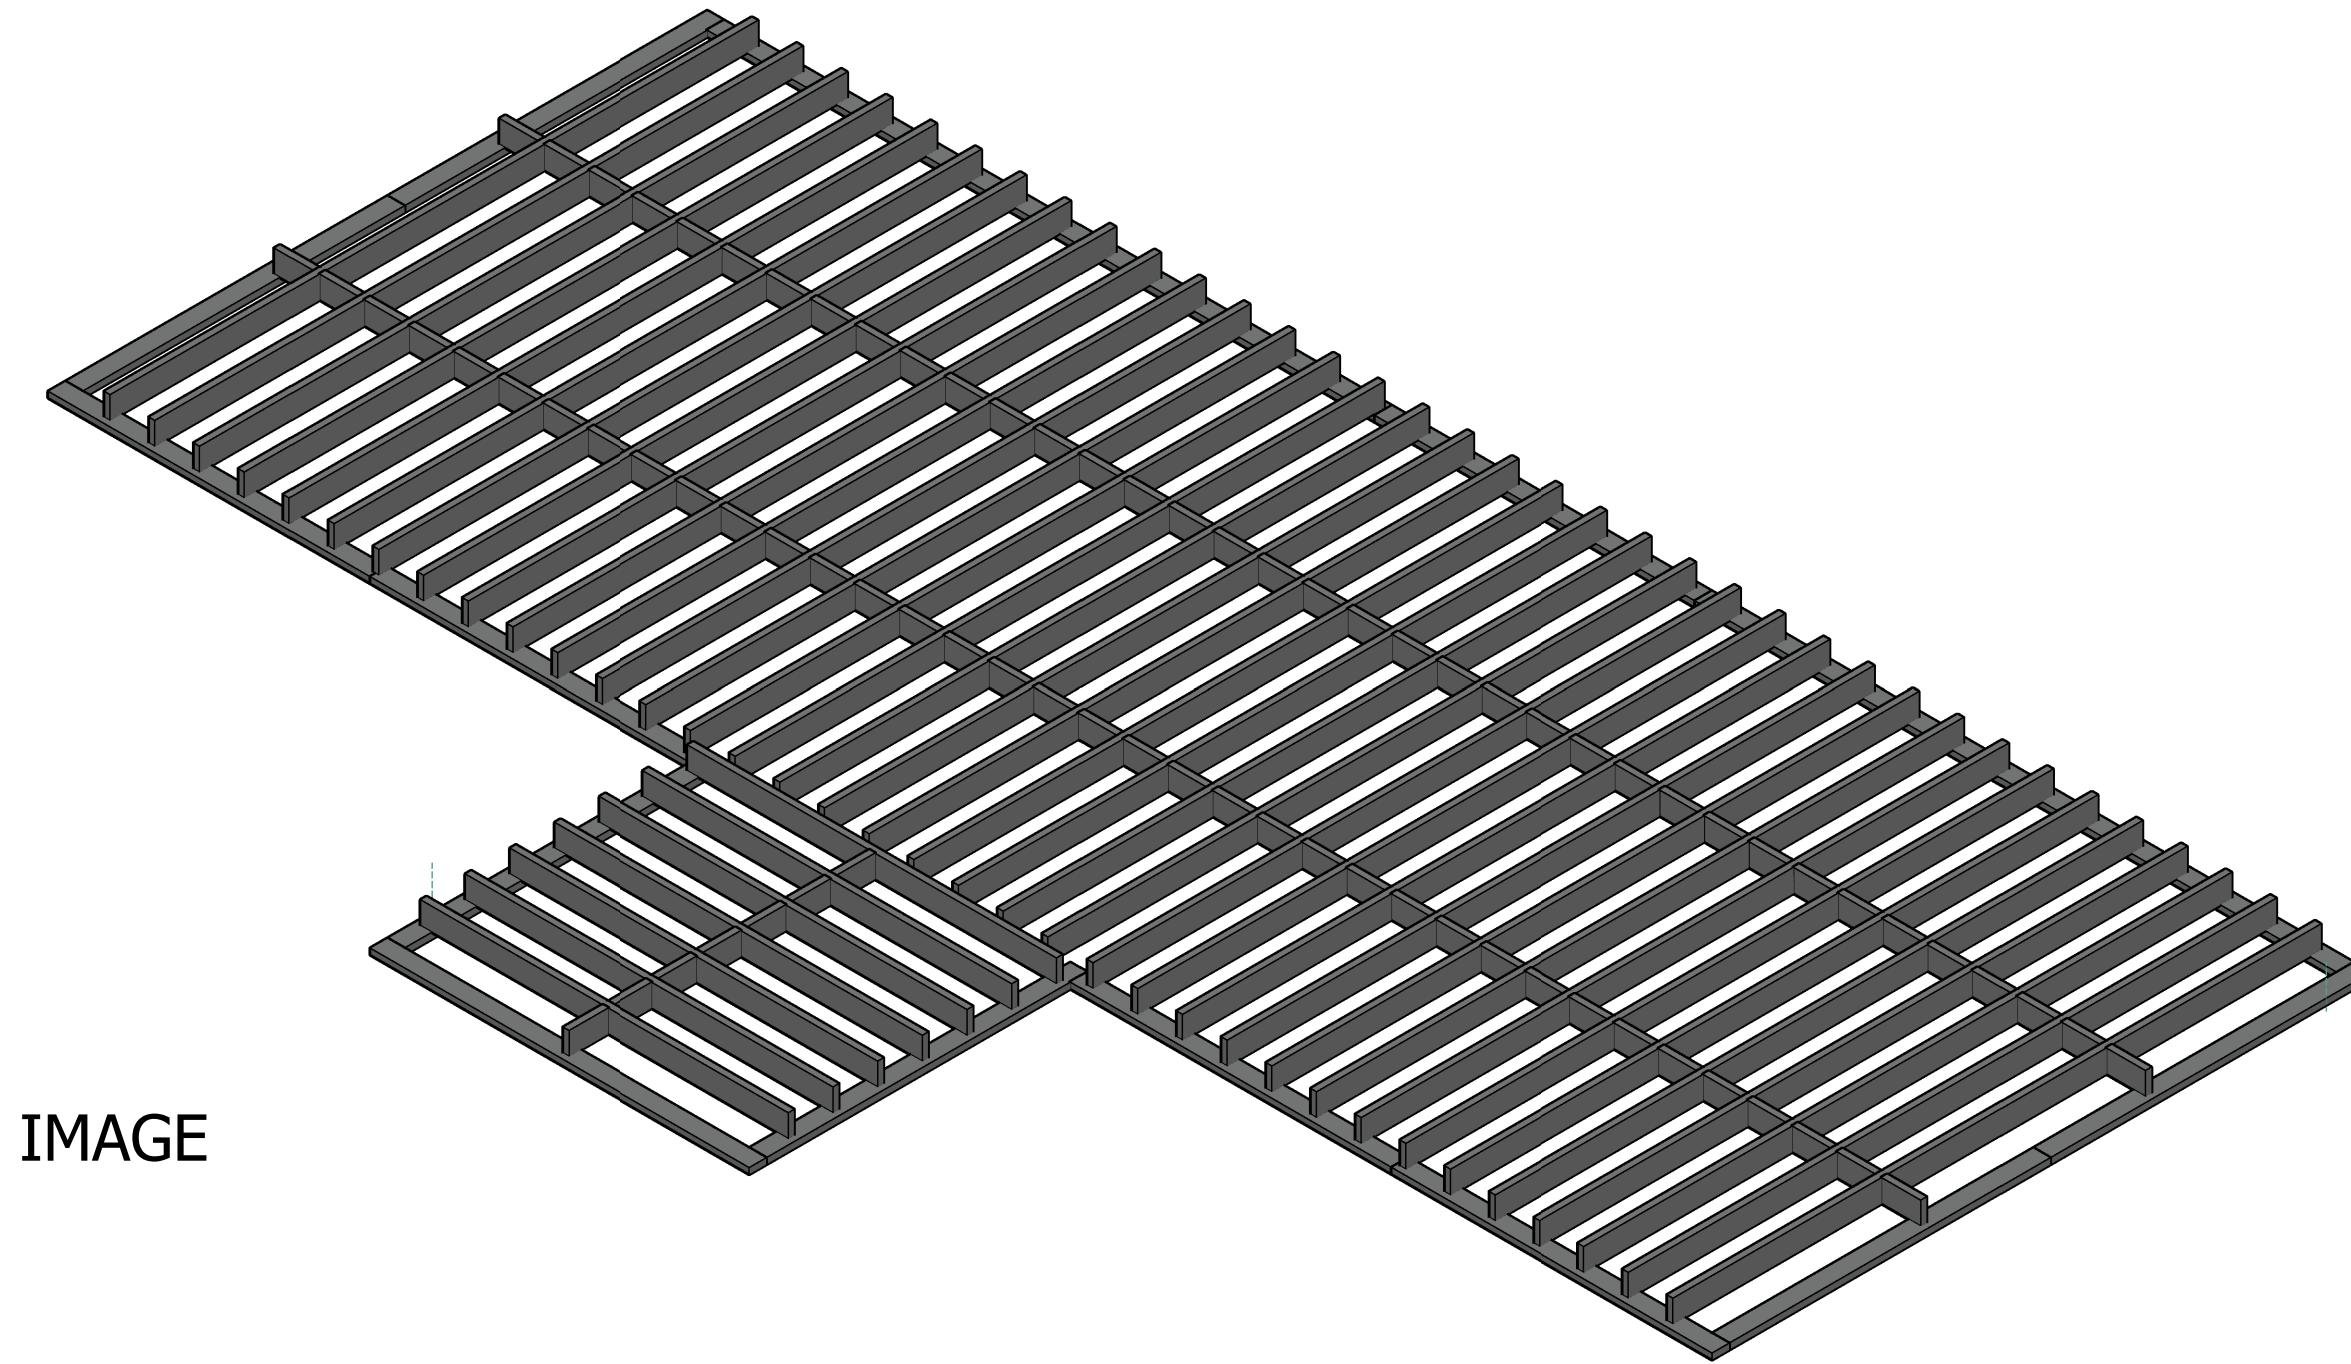

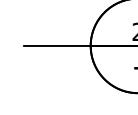 CORNER DETAIL VIEW
SCALE: 3/8"=1' 0"

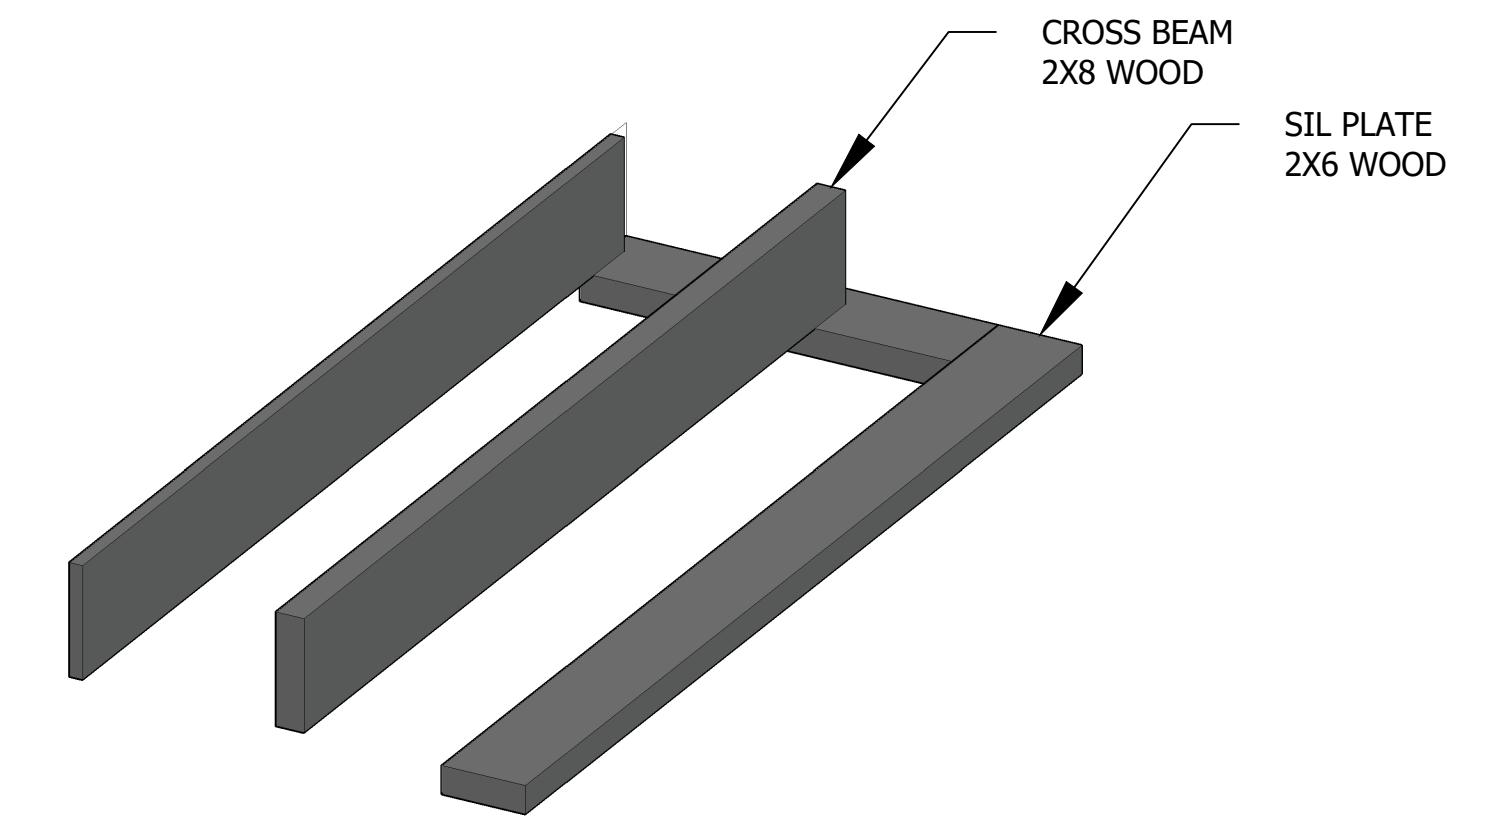

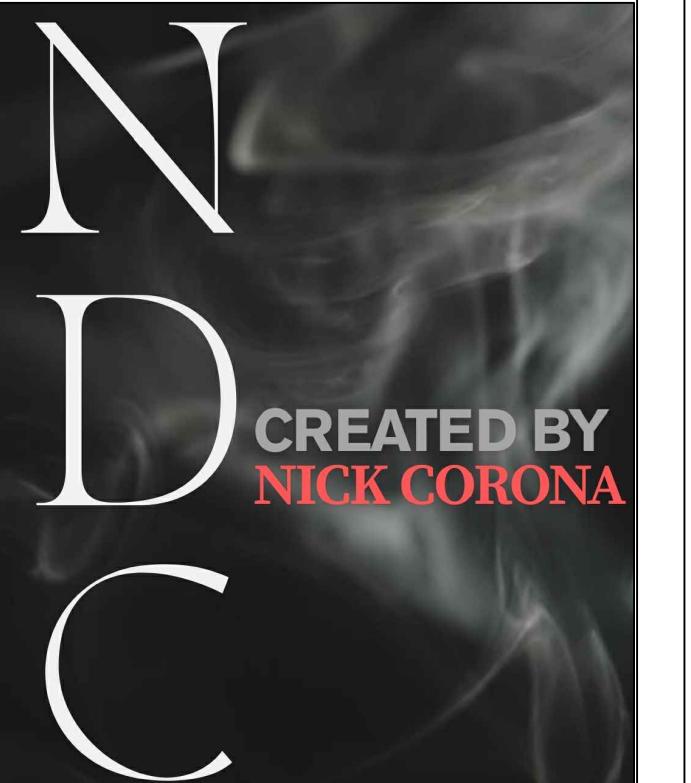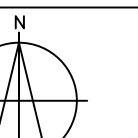No.	Revision/Issue	Date
 CREATED BY NICK CORONA		
NEW HOUSE		
ADDRESS LOCATION		
PROJECT #	0000001	
SHEET SIZE	A1	
DATE	03/31/2025	
ISSUE	BUILDING CONSENT	
		
DRAWING TITLE:	STRUCTURAL	
SHEET:	S09	
DRAWING TITLE:		

